

DRAFT — FOR DISCUSSION

LOT ACQUISITION & SPEC BUILD · OLD NORTHEAST, ST. PETERSBURG

1500 N Shore Dr NE

A courtyard residence on the park

LOT	TARGET HOME	PROFIT AT SALE, WORST–BEST	BASE CASE
14,160 sf	**4,500 sf**	**−$0.71M to +$1.77M**	**+$0.56M · +9.9%**
0.325 ac corner · park & bay view	living area · raised to ≈12 ft FFE	−10.8% to +35.8% on cost · target 15–20%	$450/sf hard · implied sale $1,450/sf · $6.53M

THE OPPORTUNITY

A 14,160 sf corner lot facing North Shore Park and Tampa Bay, acquired for $2.5M on a 0%-down seller note (3% in the Base case), interest deferred to the sale, subordinated to a spec construction loan until sale. A 4,500 sf courtyard residence raised to ≈12 ft, built to sell at about month 27.

Prepared for **Ryan Mickle** · October 11, 2026

Hero: 1695 Brightwaters Blvd NE, a comparable home, not the subject (MLS via BEX Realty). Estimates for discussion, not an appraisal.

Executive summary

The deal. Acquire the vacant 0.325-acre corner lot at 1500 N Shore Dr NE (Old Northeast, zoned NT-3, flood zone AE), facing North Shore Park and Tampa Bay, for **$2.5M on a 0%-down seller note**, with simple **interest accrued and paid at the sale closing** (no monthly payments) at **6% / 3% / 0%** in the Worst / Base / Best cases. The note stays in place until the home sells and is **subordinated** to a **spec construction loan** for 70% of the non-land project budget at 10%. Build a **4,500 sf (living area) courtyard house** raised to ≈12 ft NAVD88 and sell at about month 27. The owner's team manages the build with a licensed GC as qualifier (2% of hard cost); buyer-side commission only.

WORST CASE

$550/sf hard · $1,350/sf sale

−$0.71M

−10.8% margin on cost

Sale price	**$6.08M**
Total cost	**$6.55M**
Contingency spent	**10% of build**
Seller-note rate	**6% deferred**
Owner equity (30%)	**$0.98M**
Owner cash, total	**$1.44M**
Implied sale $/sf	**$1,350/sf · $6.08M**

BASE CASE

$450/sf hard · $1,450/sf sale

+$0.56M

+9.9% margin on cost

Sale price	**$6.53M**
Total cost	**$5.72M**
Contingency spent	**5% of build**
Seller-note rate	**3% deferred**
Owner equity (30%)	**$0.82M**
Owner cash, total	**$1.24M**
Implied sale $/sf	**$1,450/sf · $6.53M**

BEST CASE

$350/sf hard · $1,550/sf sale

+$1.77M

+35.8% margin on cost

Sale price	**$6.98M**
Total cost	**$4.94M**
Contingency spent	**1% of build**
Seller-note rate	**0% deferred**
Owner equity (30%)	**$0.67M**
Owner cash, total	**$1.04M**
Implied sale $/sf	**$1,550/sf · $6.98M**

READING THE CASES

The Base case earns +$0.56M (+9.9% on cost), below the customary 15–20% spec margin. The Best case clears it at +35.8% (+$1.77M). The Worst case loses $0.71M (−10.8%). Owner cash is ≈$1.04M–$1.44M over about 27 months, of which $0.67M–$0.98M is the 30% equity.

WHAT HAS TO BE TRUE

1. **A sale at ≈$1,450/sf or more.** In the comp set only 323 Cordova ($1,449/sf) and 1695 Brightwaters ($1,500/sf) reached that level, both with direct water access and docks. The comp median for homes of 6,000 sf or less (n = 5) is $1,347/sf (1800 N Shore, same street); the Worst case sits at the median, Base 8% and Best 15% above it, and the Best case is 3% above the highest sale (§5).
2. **Hard cost of $350–450/sf for the building.** This is at or below the low end of published builder ranges ($425–750/sf for flood-zone and waterfront work, Appendix D). Pool, hardscape and landscape ($160K) and site work ($75K) are separate. The owner's team manages the build, so a full GC fee (10–20%) is replaced by a 2% qualifier fee.
3. **The seller subordinates the note and defers its interest to the sale.** The construction lender has to accept a deferred-interest note behind its loan. Without subordination, ≈$1M+ more cash is needed up front.
4. **Timing.** Each month of delay during the build or sale costs ≈$13–39K (cash carry ≈$13–26K/mo plus $0–12.5K/mo of accruing note interest; $6.25K at Base 3%), and buyer depth above $6.5M is thin.

Living area = air-conditioned space, excluding garage, porches and lanais; the basis for all $/sf. Key assumptions and sensitivities: Appendix A.

The lot

A rare buildable corner lot on N Shore Dr NE: across from the waterfront park, a walk from downtown, among homes that seldom trade.


RARE
Buildable lots on N Shore Dr NE seldom come to market. None of the 15 land and teardown sales reviewed for 2023–2026 across Old Northeast, Coffee Pot Bayou and Snell Isle was on N Shore Dr NE.

WALKABLE PARK AND DOWNTOWN LIVING
Directly across from the waterfront park (1 min on foot). North Shore Park is a 12 min walk, the Vinoy 18 min, Beach Dr dining 22 min and the St. Pete Pier 29 min.

AMONG VALUABLE HOMES THAT RARELY TRADE
1800 N Shore sold for $6.1M in March 2024, the only single-family sale on the street in the 2024–2026 comp search. 1700 N Shore last sold in June 2015 ($1.95M) [S42]; the 6,915 sf home on it, built in 2017, carries a $7.7M county model value.


CORNER LOT WITH ALLEY ACCESS
Frontage on two streets, a 15 ft alley for the garage and services, and a ≈7,970 sf one-story building envelope under NT-3 zoning.

SIZE	ZONING	FLOOD	FRONTAGE
14,160 sf	NT-3	AE · BFE 10 ft	128.69 ft
0.325 ac corner lot	single-family · ≈7,970 sf one-story envelope	NAVD88 · VE sliver ≈507 sf (SE corner)	N Shore Dr NE · 95.09 ft on 15th Ave NE

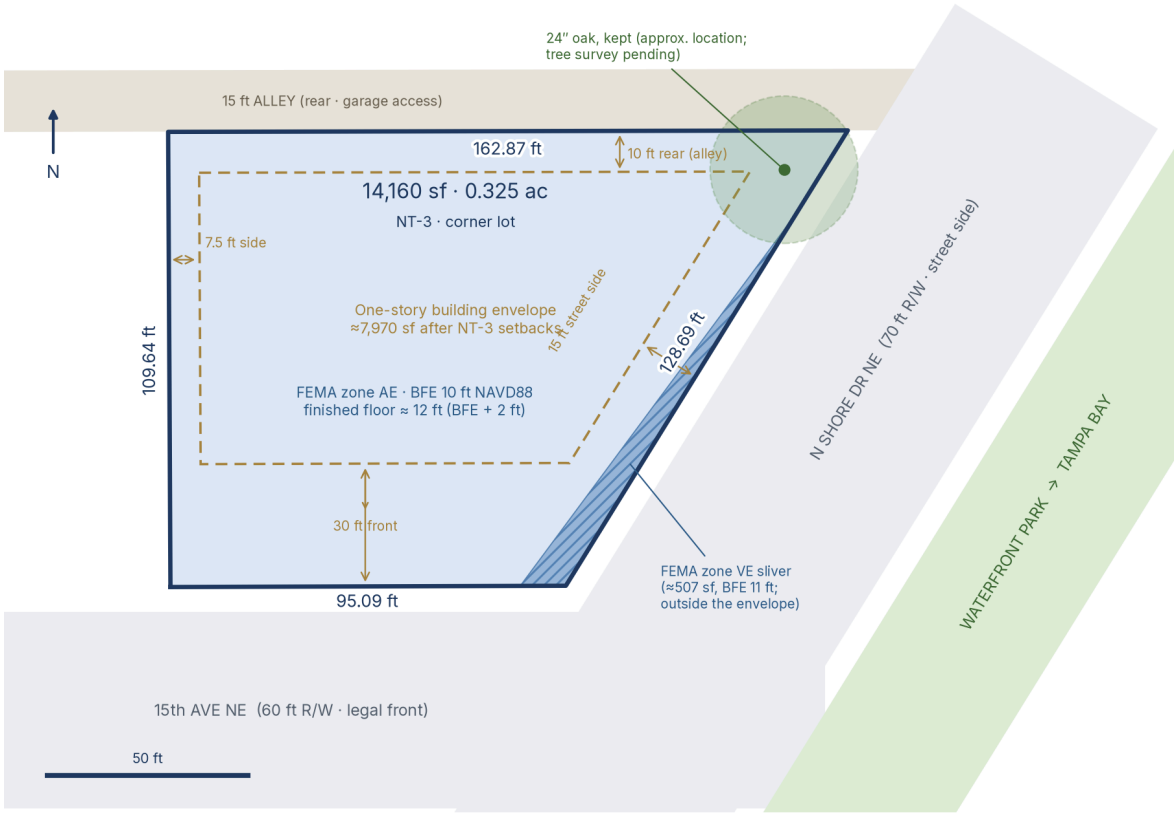

Lot diagram: survey dimensions, NT-3 one-story setbacks (dashed), FEMA AE/VE zones and the 24″ oak (approximate).

Location

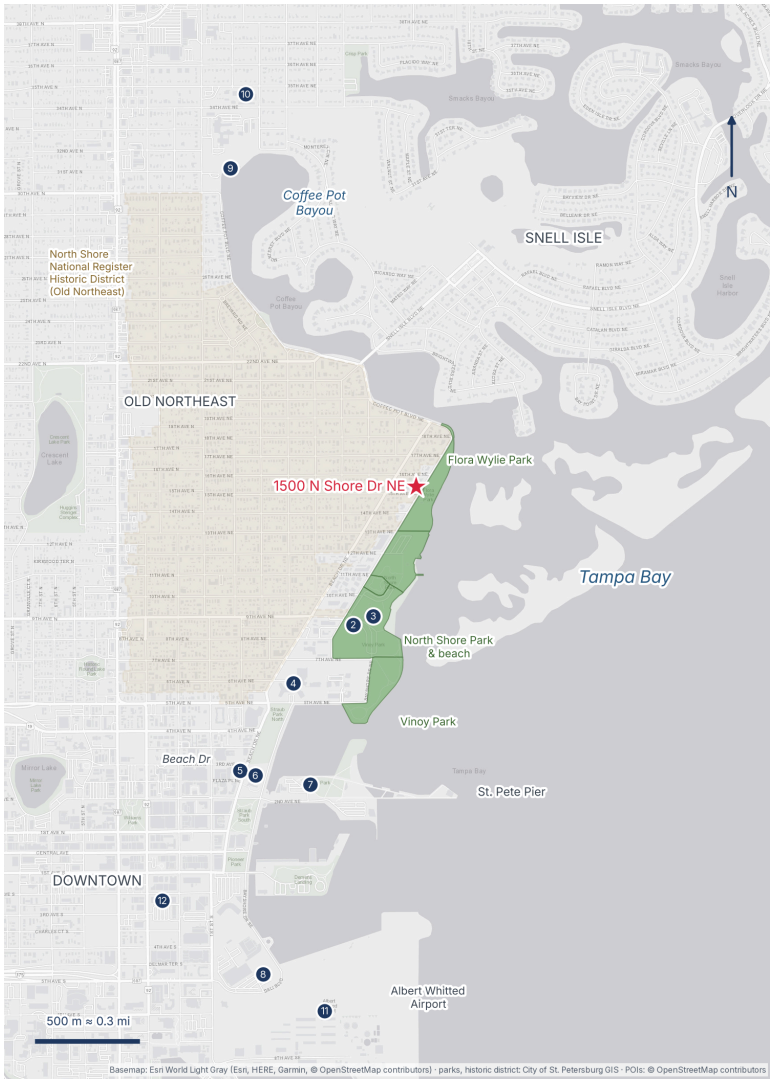

Parks green, historic district tan; times routed on OpenStreetMap; more destinations in Appendix H. Basemap © Esri, HERE, Garmin, OpenStreetMap contributors.

Walking distance from the lot

#	Destination	Walk	Drive
1	Waterfront park across N Shore Dr NE (Flora Wylie Park)	1 min · 0.04 mi	1 min · 0.04 mi
2	North Shore Park (901 N Shore Dr NE)	12 min · 0.54 mi	2 min · 0.53 mi
3	North Shore Aquatic Complex	10 min · 0.46 mi	2 min · 0.54 mi
4	The Vinoy Resort	18 min · 0.83 mi	3 min · 0.86 mi
5	Beach Dr NE dining (at 3rd Ave NE)	22 min · 1.05 mi	4 min · 1.09 mi
6	Museum of Fine Arts	23 min · 1.06 mi	4 min · 1.09 mi
7	St. Pete Pier (Pier District entrance)	29 min · 1.36 mi	5 min · 1.41 mi
9	Coffee Pot Park / Coffee Pot Bayou	28 min · 1.32 mi	5 min · 1.48 mi
—	Tampa International Airport	—	33 min · 20.6 mi

Design concepts

Five design directions drawn from top recent sales and local precedents in Old Northeast and Snell Isle. Each works with the seller's courtyard plan, the kept oak and the pool, a raised main level (≈12 ft NAVD88) on a landscaped base, and an alley garage.



Warm Florida Modern

Low, horizontal stucco-and-glass house that floats on a planted plinth.

- Flat or low-slope roofs, deep thin overhangs
- Floor-to-ceiling glass to courtyard and park
- Warm wood soffits, shellstone, bronze frames

Precedent: **323 Cordova Blvd NE** · $6.75M · **$1,449/sf** · sold Apr 2026



Modern British West Indies

Deep two-level porches and hipped roofs, updated with clean lines.

- Hipped tile or standing-seam roof, deep eaves
- Wrap-around porches and loggias on two levels
- Light stucco, wood columns, louvered shutters

Precedent: **2030 Coffee Pot Blvd NE** · $7.15M · **$1,177/sf** † · sold Sep 2025



Contemporary Coastal

Crisp two-story white volumes with large glazing and a motor court.

- Simple massing under a low tile roof
- Tall glazing and glass-rail balconies
- Motor court and grand raised entry

Precedent: **105 Cordova Blvd NE** · $8.80M · **$1,152/sf** † · sold Jun 2025



Coastal Vernacular

A refined Old-Florida form with gables and a metal roof.

- Standing-seam metal roof and gables
- Board-and-batten accents, light palette
- Wide raised entry stair and porch

Precedent: **1695 Brightwaters Blvd NE** · $8.80M · **$1,500/sf** · sold Aug 2025



Modern Mission

Clean white stucco and arched loggias, with the ornament stripped back.

- Smooth white stucco, minimal trim
- Arched loggias and a courtyard entry
- Low-pitch clay-tile or flat roofs


Precedent: **706 15th Ave NE (1935, same street)** · $1.64M · **$602/sf** · sold Apr 2025

† Over 6,000 sf; shown at actual $/sf, excluded from summary stats. Photos: MLS listing images (BEX Realty; 706 15th Ave NE via Smith & Associates) of other homes, not the subject; closed sales.

Lot value analysis

BASE PRICE	INDICATED VALUE	CLOSEST LAND COMP	COUNTY JUST VALUE
$2.50M	$2.3–2.75M	$192/sf	$1.81M
$172/sf of lot	$158–189/sf	1956 Coffee Pot · $2.8M · Aug 2026	land line $1.90M

Measure	Figure
Base price	**$2.50M = $172/sf of lot** (PCPAO 14,553 sf; $177/sf on the surveyed 14,160 sf)
Last list (context)	$2.65M (Feb 2026, $182/sf); currently on hold
County appraiser 2026	Just value $1.81M; land line $1.90M; sales-comparison figure $2.17M
Closest land comp	**1956 Coffee Pot Blvd NE**: vacant corner, bayou view across the street, no water lot; 14,588 sf; **$2.8M (Aug 2026), $192/sf**
Other land comps	Water lot across the street (upland $/sf): median $164 ($147–189). Direct seawall: median $141 ($118–230). Inland Old NE: $112
Indicated land value	**$2.3–2.75M ($158–189/sf)**

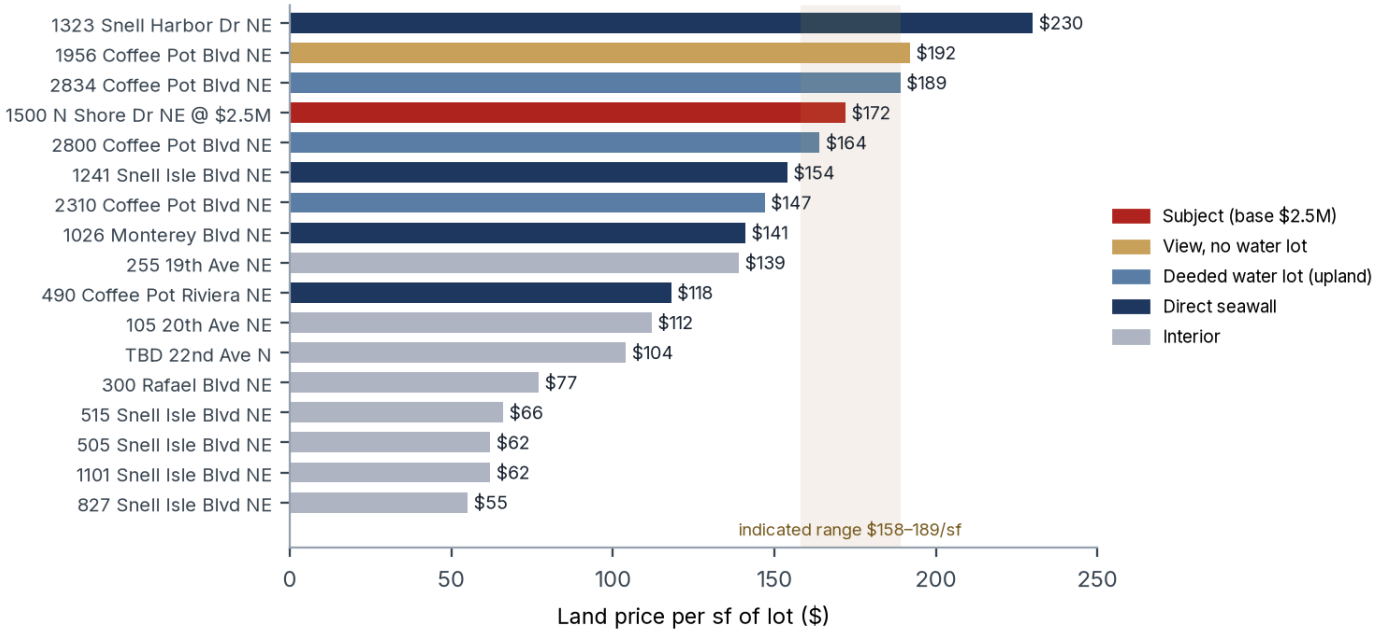

Land comps, $ per sf of lot (2023–2026). Water-lot comps on upland area.


- **Position in the range.** $2.5M ($172/sf) falls inside the indicated range, ≈$0.3M below the closest analogue (1956 Coffee Pot, $192/sf), and at ≈1.4× the county's just value.
- **Scarcity.** No other land sale on N Shore, Beach Dr or Bayshore was found for 2023–2026. The lot is a large corner with an alley, faces the park and bay, is walkable to downtown and the Vinoy, and is outside any local historic district.
- **Constraints.** There is no boat access, a public park (and its events) is in front, and the lot is in flood zone AE and evacuation zone A. Each of these sets it apart from the water-access comps at the top of the home market.

Finished home value

COMP SET	$/SF RANGE	MEDIAN	CASE VALUES, 4,500 SF
n = 5	$979–1,500	$1,347/sf	$6.08–6.98M
≤ 6,000 sf · 2015+ waterfront + 1800 N Shore · 2024–26	closed sales	homes ≤ 6,000 sf · ≈ Worst case	$1,350–1,550/sf

Comp set: closed sales of 2015-or-newer waterfront homes in Old Northeast and Snell Isle, plus 1800 N Shore, limited to homes of **6,000 sf living area or less** (n = 5, 2024–2026). $/sf: **$979–1,500; median $1,347**. The three pro forma sale cases sit at the top of this range, where the newest, best-located product trades: Worst $1,350 is at the median (≈1800 N Shore, 3rd of 5); Base $1,450 is 8% above (≈323 Cordova, 2nd of 5); Best $1,550 is 15% above the median and 3% above the highest sale (1695 Brightwaters, $1,500).

Sale $/sf	Basis	Value at 4,500 sf
$1,347	Comp median, homes ≤ 6,000 sf (context; ≈ Worst case)	$6.06M
$1,350	**Worst case** (≈1800 N Shore, $1,347/sf, same street)	**$6.08M**
$1,450	**Base case** (≈323 Cordova, $1,449/sf, closest in size)	**$6.53M**
$1,550	**Best case** (above 1695 Brightwaters, $1,500/sf; ≈the listing agent's $7M)	**$6.98M**

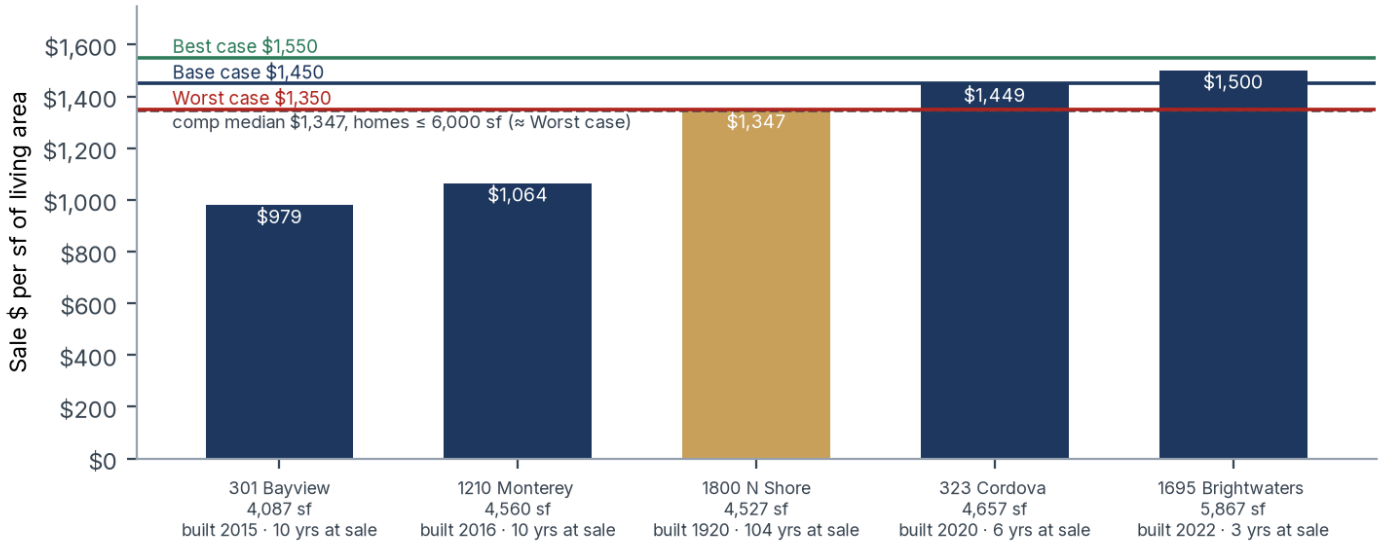

Comps of 6,000 sf or less, sale $ per sf of living area, with year built and age at sale, and the three pro forma sale cases

Risks and counterpoints to the value estimate

- **No dock or open-water frontage.** Every sale above $1,350/sf has direct open-bay or harbor frontage with a dock, or extensive water lots; this lot has none. 2030 Coffee Pot, with water lots across the street, sold at $1,177/sf.
- **$7M+ takes more size than the plan.** Every $7M+ sale in the set is 5,867 sf or larger. At 4,500–4,700 sf the top is $6.1–6.75M; $7M at 4,500 sf implies $1,556/sf, above every sale in the set.
- **New-construction premium is a tendency, not a measured fact.** Base and Best lean on it: among the five comps of 6,000 sf or less the newest sold highest (1695 Brightwaters, 3 years old, $1,500/sf; 323 Cordova, 6 years, $1,449/sf) against $979–1,064/sf for two 10-year-old homes, yet brand-new homes over 6,000 sf sold at only $882–1,177/sf.
- **Upside on this street is unproven.** 1700 N Shore's $7.7M county model value and the park, bay and downtown setting may support more, but neither is a closed sale, and the comp set is only five homes.

High-end comps at a glance



1695 Brightwaters Blvd NE

Snell Isle · sold Aug 2025 · built 2022 · age at sale 3

$8.80M **$1,500/sf** **5,867 sf**

147 ft open-bay frontage; dock, 2 lifts
Modern coastal; standing-seam metal roof; raised entry



323 Cordova Blvd NE

Snell Isle · sold Apr 2026 · built 2020 · age at sale 6

$6.75M **$1,449/sf** **4,657 sf**

Snell Isle Harbor
Warm modern; flat roofs, glass; infinity pool; closest in size



1800 N Shore Dr NE

Old NE, same street · sold Mar 2024 · built 1920 · age at sale 104

$6.10M **$1,347/sf** **4,527 sf**

360 ft via four water lots across the park; dock
Palm Beach Revival, restored; street record



2030 Coffee Pot Blvd NE

Old NE · sold Sep 2025 · built 2019 · age at sale 6

$7.15M **$1,177/sf†** **6,076 sf**

Two water lots across the street
West Indies; wrap porches; courtyard pool



105 Cordova Blvd NE

Snell Isle · sold Jun 2025 · built 2024–25 · age at sale 0–1 (new)

$8.80M **$1,152/sf†** **7,640 sf**

Snell Isle Harbor; dock
Coastal contemporary; sold after price cuts



1075 31st Ter NE

Snell Isle Estates · sold Apr 2026 · built 2026 · age at sale 0

$7.95M **$1,174/sf†** **6,774 sf**

≈155 ft on Smacks Bayou; lift
Contemporary coastal; terraces, pool

- **Water access sets the $/sf ceiling:** the two highest ($1,449–1,500/sf) have direct harbor or open-bay frontage with docks.
- **Size drives $7M+:** every $7M+ sale is 5,867 sf or larger.

† Over 6,000 sf; shown at actual $/sf, excluded from summary stats. Photos: MLS listing images via BEX Realty (comparable homes, not the subject). All comps: Appendix K.


Pro forma: three cases

Worst: $550/sf hard cost, sale at $1,350/sf. Base: $450/sf, $1,450/sf. Best: $350/sf, $1,550/sf. Hard cost $/sf covers the **building only** (including elevated construction). It **excludes** pool, hardscape and landscape ($160K) and site work ($75K), which are separate lines, with a 10% contingency on all three. The full 10% contingency stays in the budget, the loan sizing and owner cash; the share actually spent varies by case: **Worst 10%, Base 5%, Best 1% of the build budget**.

Results by case

4,500 sf	Worst case	Base case	Best case
Hard cost $/sf (building only)	$550	$450	$350
Sale $/sf	$1,350	$1,450	$1,550
Contingency spent (% of build budget)	10% · $0.27M	5% · $0.11M	1% · $0.02M
Seller-note rate (0 down, deferred to sale)	6%	3%	0%
GC qualifier fee (2% of hard cost)	$49,500	$40,500	$31,500
Total cost before sale	$6.55M	$5.72M	$4.94M
Sale price	$6.08M	$6.53M	$6.98M
Net profit at sale	**−$0.71M**	**+$0.56M**	**+$1.77M**
Margin on cost	**−10.8%**	**+9.9%**	**+35.8%**
Owner cash in, total	$1.44M	$1.24M	$1.04M
Seller-note payoff at sale (principal + interest)	$2.84M	$2.67M	$2.50M

Build budget = building hard cost + site work + pool/hardscape. A 0% note for 3 years needs the seller's agreement; the 27-month plan leaves 9 months before a 36-month maturity. 6% vs. 0% and draw pace: Appendix B. GC: a licensed qualifier at 2% of hard cost [S43]; the owner's team manages the build, with general conditions inside hard $/sf. The arrangement must be bona fide, with the qualifier supervising the work (Fla. Stat. §489.1195) [S44].

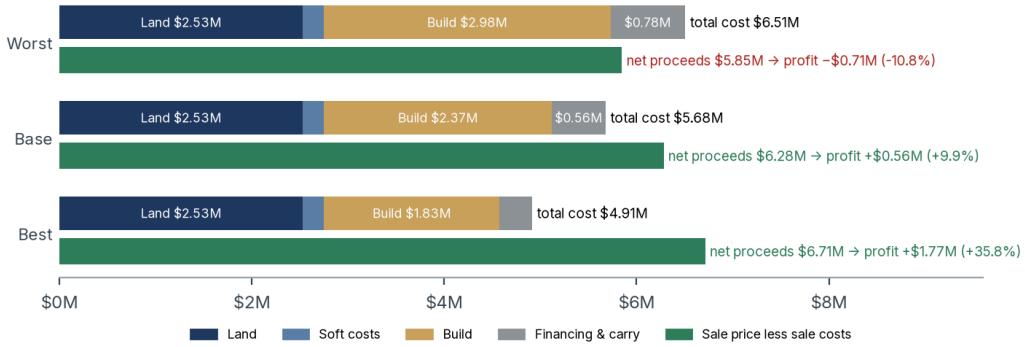

Total cost by category vs. net sale proceeds, by case

Budget and sensitivity

Sources & uses by case

Uses, 4,500 sf	Worst	Base	Best
Land			
Land (seller note, 0% down)	$2,500,000	$2,500,000	$2,500,000
Land closing costs	$28,750	$28,750	$28,750
Soft costs			
Design, engineering, survey	$165,000	$165,000	$165,000
Permits & impact fees	$40,000	$40,000	$40,000
Utilities	$15,000	$15,000	$15,000
Build			
Hard cost, building only ($550 / $450 / $350/sf)	$2,475,000	$2,025,000	$1,575,000
Site work & fill	$75,000	$75,000	$75,000
Pool, hardscape, landscape	$160,000	$160,000	$160,000
Contingency spent (10% / 5% / 1% of build budget)	$271,000	$113,000	$18,100
GC qualifier fee (2% of hard cost)	$49,500	$40,500	$31,500
Financing & carry			
Construction loan closing	$68,021	$59,025	$50,029
Seller-note interest (6% / 3% / 0%, accrued, paid at sale)	$337,500	$168,750	$0
Construction interest (10%)	$199,093	$168,223	$137,353
Property tax (27 mo)	$81,283	$81,283	$81,283
Insurance (builder's risk, GL, flood)	$89,572	$78,435	$67,298
Total cost before sale	**$6,554,720**	**$5,717,966**	**$4,944,312**
Sources			
Seller note (subordinated; repaid at sale)	$2,500,000	$2,500,000	$2,500,000
Seller-note interest, accrued (paid from sale proceeds)	$337,500	$168,750	$0
Spec construction loan (70% of non-land budget)	$2,275,350	$1,922,550	$1,569,750
Owner cash	**$1,441,870**	**$1,239,666**	**$1,037,462**
Less: contingency not spent (undrawn; released at sale)	$0	−$113,000	−$162,900

Net profit and margin on cost: hard cost vs. sale price

Hard cost ↓ · Sale →	$1,350/sf Worst-case sale	$1,450/sf Base-case sale	$1,550/sf Best-case sale	Break-even
$350/sf Best-case cost	**+14.4%** +$0.73M	**+22.8%** +$1.17M	**+31.3%** +$1.60M	**$1,180/sf**
$450/sf Base-case cost	**+2.3%** +$0.13M	**+9.9%** +$0.56M	**+17.4%** +$1.00M	**$1,320/sf**
$550/sf Worst-case cost	**−8.4%** −$0.54M	**−1.6%** −$0.10M	**+5.1%** +$0.33M	**$1,474/sf**

≤ −20% · −10% · 0% · +7% · ≥ 15% target · *Outlined cells = the three cases (diagonal)*

Every cell uses the Base 3% note rate and the 2% qualifier fee; contingency spent 1% / 5% / 10% of the build budget down the hard-cost rows.

- **±$50/sf of hard cost** moves Base profit by ≈$0.26M; **±$50/sf of sale price** by ≈$0.22M. The loan rate (8.5–11.5%) moves it only ≈$25K either way (Appendix F).
- **15% margin** needs ≈$1,518/sf at Base cost, ≈$1,313/sf at Best cost and ≈$1,740/sf at Worst cost.

Owner cash and monthly carry

The construction loan funds 70% of the non-land project budget: design and engineering, permits, utilities, the building, site work, pool and hardscape, and the full 10% contingency. The owner funds the other 30%, plus costs the model treats as paid in cash: land and loan closing, construction interest (paid monthly; no interest reserve), property tax and insurance. The seller-note interest is not paid monthly. It accrues as simple interest at 6% / 3% / 0% by case (Base: $2.5M × 3% × 27/12 = $168,750; Worst $337,500; Best $0) and is paid with the $2.5M principal at the sale closing, so owner cash is the same at any note rate.

Owner cash, 4,500 sf	Worst	Base	Best
Hard cost, building	$2,475,000	$2,025,000	$1,575,000
Site, pool/hardscape and 10% contingency (full)	$506,000	$461,000	$416,000
Design/engineering/survey, permits, utilities	$220,000	$220,000	$220,000
Non-land project budget (loan basis)	**$3,250,500**	**$2,746,500**	**$2,242,500**
Construction loan (70%)	$2,275,350	$1,922,550	$1,569,750
Owner equity (30%)	**$975,150**	**$823,950**	**$672,750**
+ Land and loan closing (cash)	$96,771	$87,775	$78,779
+ Construction interest, paid monthly	$199,093	$168,223	$137,353
+ Property tax, 27 months	$81,283	$81,283	$81,283
+ Insurance (builder's risk, GL/flood)	$89,572	$78,435	$67,298
Total owner cash over 27 months	**$1,441,870**	**$1,239,666**	**$1,037,462**
Alternative: lender funds interest reserve, loan fees and builder's risk			
Loan basis incl. financed interest and fees	$3,613,392	$3,054,007	$2,494,622
Owner equity (30%)	$1,084,018	$916,202	$748,387
+ Land closing, tax, GL/flood (cash)	$132,533	$132,533	$132,533
Total owner cash (alternative)	**$1,216,550**	**$1,048,735**	**$880,920**
Net profit (alternative vs. model)	−$0.74M (−$0.03M)	+$0.54M (−$0.02M)	+$1.75M (−$0.02M)
At sale: seller-note payoff (principal + accrued interest)	$2,837,500	$2,668,750	$2,500,000

Monthly carry paid by the owner

Phase	Worst	Base	Best	Components
Design & permit (months 1–9)	$3,844	$3,844	$3,844	Property tax ≈$3,010 + GL/flood ≈$833
Construction (months 10–24), average	$17,051	$14,962	$12,873	+ construction interest (S-curve draws, avg 50% drawn) + builder's risk
Marketing & sale (months 25–27)	$26,531	$22,973	$19,414	Loan fully drawn + tax + insurance
Memo: seller-note interest (accrues, not paid)	$12,500	$6,250	$0	6% / 3% / 0%; paid at the sale closing

LENDER POINTS TO NEGOTIATE

- **Subordinated, deferred-interest seller note.** A construction lender has to accept the $2.5M note, plus its growing accrued interest, sitting behind its first lien. This is the key negotiation point with both the seller and the lender.
- **Land equity.** The note is 0% down, so there is no cash land equity. Some lenders size on total cost including land, or cap combined debt (note + accrued interest + loan) at 65–75% of completed value. At 70% of total cost including the land, the Base owner equity would be ≈$1.57M instead of $0.82M. A lender may also credit land equity only if the appraisal exceeds the $2.5M price.

Path to $350/sf

What a $350/sf hard cost ($1.575M for 4,500 sf of living area, building only) would require, and whether it fits a home meant to sell at $1,450–1,550/sf. Pool, hardscape and landscape ($160K), site work ($75K), permits and impact fees (soft costs) and the 10% contingency stay outside this number; the 2% GC qualifier fee sits in the §6 pro forma, not in this number.

Budget by category (building only)

Category (building only)	$350/sf case	$/sf	$450/sf (Base)	$/sf	$550/sf (Worst)	$/sf
Foundation & elevation	$225,000	$50	$245,000	$54	$275,000	$61
Structure & envelope	$475,000	$106	$590,000	$131	$710,000	$158
MEP (mechanical, electrical and plumbing: HVAC, wiring/panels, water and drain lines)	$237,000	$53	$297,000	$66	$372,000	$83
Interior shell	$80,000	$18	$97,000	$22	$117,000	$26
Interior finishes	$180,000	$40	$247,000	$55	$307,000	$68
Kitchen, baths & fixtures	$225,000	$50	$345,000	$77	$455,000	$101
Stairs & garage	$62,000	$14	$85,000	$19	$104,000	$23
General conditions	$91,000	$20	$119,000	$26	$135,000	$30
Total hard cost, building only	**$1,575,000**	**$350**	**$2,025,000**	**$450**	**$2,475,000**	**$550**

Top levers: savings vs. the $450/sf Base budget (ranges overlap; not additive)

1. **Spec-level finishes with targeted splurges: ≈$150–220K.** Spend in the kitchen, primary bath, entry and the view wall; standardize everything else (cabinets, counters, appliances, flooring, tile, trim, fixtures, lighting).
2. **Simple massing and a value-engineered plan: ≈$70–140K.** Rectangular footprint, minimal corners, one roof form, stacked plumbing, standard spans; a repeat or design-build plan reviewed for cost before permit.
3. **Direct trade buying and competitive bids: ≈$60–120K.** Three or more bids per trade; buy appliances, tile, fixtures, lighting and windows direct at trade pricing.
4. **Glass strategy: ≈$40–90K.** Hold openings to ≈1,100 sf in standard sizes; 8–12 ft sliders instead of pivot or multi-slide pocket walls; value-tier impact line.
5. **Foundation choice for the 8 ft raise: ≈$30–80K.** Geotech first: spread footings on compacted fill vs. piles; CMU (concrete masonry unit, i.e. concrete block) ground level with garage vs. structural columns; precast or filigree elevated deck vs. cast-in-place.

Owner management already replaces a 10–20% GC fee with the 2% qualifier fee in the pro forma; the remaining saving here is leaner general conditions (≈$25–50K). Skipping the elevator saves ≈$35–45K but is not recommended (Appendix M).

REALITY CHECK

- **Local ranges.** Tampa Bay production builders run ≈$180–260/sf and semi-custom ≈$250–350/sf (Toll Brothers ≈$310–380) [N6, N7]; luxury custom runs $425–750+/sf, with coastal and flood-zone work 15–25% higher [N7]. St. Pete flood-zone custom builders quote $425–525/sf (FEMA flood zone AE) [S1]; A2 Construction quotes $320–520/sf for elevated waterfront, before the GC fee [S3]. City permit declarations for nearby new homes run $177–347/sf, a floor rather than a budget (Appendix D).
- **Verdict.** $350/sf is reachable only as a disciplined, owner-managed, semi-custom build: simple massing, standard glass and spec-level finishes with a few splurges. That is below what the comps that set $1,450–1,550/sf were built to, and the main risk is the sale price, not the build.
- **What the miss costs.** At $350/sf hard, net profit is +$1.60M (+31.3%) at $1,550/sf, +$1.17M (+22.8%) at $1,450/sf, +$0.73M (+14.4%) at $1,350/sf and +$0.30M (+5.9%) at $1,250/sf. A $400/sf build selling at $1,450/sf earns +$0.87M (+16.1%). (Base 3% note; 2% qualifier fee; contingency spent 1% of the build budget at $350/sf, 3% at $400/sf.)
- **Finish floor at this price.** Buyers at $6M+ expect an elevator, impact glass with large sliders to the view, 10 ft+ ceilings, a designer kitchen with a pro-style or integrated appliance suite and stone counters, a spa-style primary bath, one premium floor material throughout, a whole-house generator and a pool with outdoor kitchen (judgment based on the comp set in §5).

Estimates from NAHB category shares, Florida glazing/elevator pricing and local builder ranges; no bids. Line items and sources [N1–N7]: Appendix M.

APPENDIX

Supporting detail

A. Pro forma key assumptions, basis and detailed budget

B. Financing: seller note, subordination, construction loan and draw schedule

C. Carry and cash flow by phase

D. Build cost research and permit valuations

E. Tax and insurance assumptions

F. Rate sensitivity: construction loan at 8.5% and 11.5% (4,500 sf)

G. Property, zoning, flood and city measurements

H. Aerials, lot details and distances

I. Seller documents

J. Listing agent comp sheet

K. Full comps tables and high-end profiles

L. Risks, timeline and open questions

M. Path to $350/sf: line-item budget and levers

N. Sources

Third-party content: seller documents and the listing agent's comp sheet are reproduced as provided. Figures are desk estimates for discussion, not an appraisal or design.


A. Pro forma key assumptions, basis and detailed budget

KEY ASSUMPTIONS BY CASE

Key assumption	Worst	Base	Best	Base-case profit sensitivity
CHANGES BY CASE				
Hard cost $/sf (building only)	$550	$450	$350	−$266K / +$266K (±$50/sf)
Sale $/sf	$1,350	$1,450	$1,550	−$217K / +$217K (±$50/sf)
Contingency spent (% of build budget)	10%	5%	1%	−$113K / +$113K (0–10%; Base 5%)
Seller-note rate (0 down, deferred to sale)	6%	3%	0%	−$169K / +$169K (0–6%; Base 3%)
SAME INPUTS IN EVERY CASE				
Lot price	$2.5M	$2.5M	$2.5M	−$268K / +$268K (±$250K)
Size (living area)	4,500 sf	4,500 sf	4,500 sf	−$432K / +$432K (±500 sf), $/sf held
Architect / engineering	$150K	$150K	$150K	−$54K / +$54K (±$50K)
Pool, hardscape, landscape	$160K	$160K	$160K	−$58K / +$58K (±$50K)
Insurance during construction (follows build budget)	$89,572	$78,435	$67,298	−$30K / +$30K (±0.5 pt · ±$5K/yr)
Construction loan	10%, 70% LTC	same	same	rate −$25K / +$25K (±1.5 pts); LTC −$31K / +$16K (65–80%)
Timeline	27 mo	27 mo	27 mo	build −$64K / +$64K (±3 months)

Insurance = builder's risk 1.5%/yr of the build budget for 18 months + general liability/flood $10K/yr for 27 months. Sensitivities show the Base-case profit change at the low / high end of each range; size assumes $/sf holds, which is unlikely, since larger homes tend to sell for less per sf.

Which assumptions matter most (Base case, net profit +$0.56M)

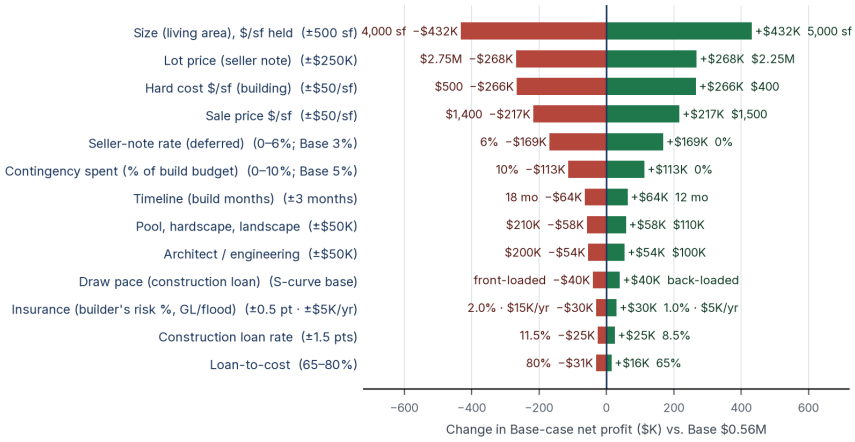

Change in Base-case net profit when each assumption moves across the range shown, all else held at Base

WHY 4,500 SF

Among the 15 closed sales in the comp set, five are 4,000–5,000 sf, and two of those closed above $5M: 323 Cordova ($6.75M, 4,657 sf, Apr 2026) and 1800 N Shore ($6.10M, 4,527 sf, Mar 2024). The other five sales above $5M are 5,867–7,640 sf. At 4,500 sf the Base price ($6.53M) stays below the $7M+ tier, where recent buyers bought larger homes with docks. The comp set is a curated sample, not an MLS census; absorption (months of supply above $5M in 33704) has not been measured and is a diligence item.

Basis: build to sell, 4,500 sf living area. Headline = **net profit and margin on cost at sale** in three cases (Worst $550/sf hard, $1,350/sf sale; Base $450, $1,450; Best $350, $1,550), benchmarked to the customary **15–20% spec margin on cost**. **GC: a licensed qualifier at 2% of hard cost**; the owner's team manages the build and carries general conditions inside hard $/sf. Sale costs are **buyer-side commission only (2.75%)** plus deed doc stamps (0.70%) and owner's title [S9, S14, S20]. Timeline [A]: design/permit 9 months + build 15 + sale 3 = **27 months**.

Sources and uses with basis (construction loan 10.0%)

Uses, 4,500 sf	Worst	Base	Best	Basis
Land				
Land (seller note, 0% down)	$2,500,000	$2,500,000	$2,500,000	$2.5M base (last list $2.65M = context); note repaid at sale
Land closing costs	$28,750	$28,750	$28,750	0.35% + 0.2% on note [S9] + $15K [A]
Soft costs				
Design, engineering, survey	$165,000	$165,000	$165,000	$150K [A; 8–12% of hard, S2] + $15K
Permits & impact fees	$40,000	$40,000	$40,000	$40K [A; $17–28K in S1]
Utilities	$15,000	$15,000	$15,000	$15K [A]
Build				
Hard cost, building only ($550 / $450 / $350/sf)	$2,475,000	$2,025,000	$1,575,000	$350 / $450 / $550 per sf of living area by case; building only (Appendix D)
Site work & fill	$75,000	$75,000	$75,000	$75K [A; S1, S4]
Pool, hardscape, landscape	$160,000	$160,000	$160,000	$160K [S1, S7, S8]

Uses, 4,500 sf	Worst	Base	Best	Basis
Contingency spent (10% / 5% / 1% of build budget)	$271,000	$113,000	$18,100	10% of hard + site + pool budgeted (loan sizing, owner cash); spent 10% / 5% / 1% of the build budget by case
GC qualifier fee (2% of hard cost)	$49,500	$40,500	$31,500	License-holder qualifier; owner manages the build [S43, S44]
Financing & carry				
Construction loan closing	$68,021	$59,025	$50,029	2% + $10K + 0.55% of the loan (70% of non-land budget) [S9, S11]
Seller-note interest (6% / 3% / 0%, accrued, paid at sale)	$337,500	$168,750	$0	$2.5M × 6% / 3% / 0% × 27/12, simple; accrued, paid at sale closing
Construction interest (10%)	$199,093	$168,223	$137,353	10.0% on the monthly outstanding balance: S-curve draws over 15 months (avg 50% drawn), full balance for the 3-month sale
Property tax (27 mo)	$81,283	$81,283	$81,283	PCPAO just value $1.81M × 19.9197 mills [S13]
Insurance (builder's risk, GL, flood)	$89,572	$78,435	$67,298	Builder's risk 1.5%/yr [S19] + $10K/yr GL/flood [A]
Total cost before sale	**$6,554,720**	**$5,717,966**	**$4,944,312**	
Sources				
Seller note (subordinated; repaid at sale)	$2,500,000	$2,500,000	$2,500,000	Repaid from sale proceeds
Seller-note interest, accrued (paid from sale proceeds)	$337,500	$168,750	$0	$2.5M × 6% / 3% / 0% × 27/12, simple
Spec construction loan (70% of non-land budget)	$2,275,350	$1,922,550	$1,569,750	Design, permits, build and full 10% contingency
Owner cash	**$1,441,870**	**$1,239,666**	**$1,037,462**	30% equity + closing, construction interest, tax, insurance
Less: contingency not spent (undrawn; released at sale)	$0	−$113,000	−$162,900	Budgeted for the lender, not spent in Base/Best

B. Financing: seller note, subordination, construction loan and draw schedule

Land and seller note

Item	Figure
Base land price	**$2.50M** ($172/sf of surveyed land)
Last list price (context)	$2.65M (Feb 2026; $182/sf). Status: hold
County appraiser, 2026	Market (just) value $1.81M · land line $1.90M · sales-comparison figure $2.17M
Best same-type land comp	1956 Coffee Pot Blvd NE: vacant corner lot, view across the street, no water lot, 14,588 sf, sold $2.8M in Aug 2026 ($192/sf)
Other land comps ($/sf)	Direct seawall: median $141 (range $118–230). Deeded water lot, upland only: median $164 ($147–189). Inland Old NE: $112
Indicated land value	$2.3M–$2.75M ($158–189/sf); $2.5M sits mid-range
Seller note [A]	**0% down**; note **$2.5M**, interest **accrued, not paid monthly** at 6% / 3% / 0% by case (Base 3%: $6,250/month, ≈$168,750 over 27 months simple), paid with the principal from sale proceeds
Note closing costs	Doc stamps on the note 0.35% ($8,750) + intangible tax 0.2% ($5,000) [S9]
Key structural issue	The note stays in place through the build only if the seller **subordinates** it to the construction lender (Appendix B). This is the central negotiation point

Land: seller note through sale (base case). $2.5M at 3% in the Base case (6% Worst, 0% Best), **0% down, interest accrued and paid at the home sale closing** (no monthly payments); principal and ≈$168,750 of Base-case interest are repaid from sale proceeds. It is **not** retired by the construction loan.

Key negotiation point: subordination. A construction lender requires first lien [S32, S36]. Keeping the seller note in place through the build requires the **seller to subordinate the note** to the construction lender (recorded subordination agreement), or a lender willing to sit **behind** it in second position, which few lenders accept [S36]. A subordinated seller risks being wiped out in a foreclosure, so expect the seller to ask for something in return (a higher rate, a shorter term, personal guarantee or a price adjustment). If the seller will not subordinate, the fallback is a construction loan that pays off the note at closing, which requires a lender that finances land plus vertical and roughly **$1M+ more owner cash** up front.

Spec construction loan (market, October 2026):

- **Prime 7.00%** (WSJ, effective Sep 17, 2026) [S23].
- **Florida spec programs:** Normandy, prime + 2.95–3.95% (≈**9.95–10.95%**), 1.5–2.0% fee, **lesser of 75% LTC or 65% of appraised value**, 12-month IO term [S11]. Capital Kings (Oct 2026): **9.99–11.49%** IO, 2% origination, 85–90% of cost capped at **65–75% of completed value** [S37]. Jaken Finance: 8.99–13.5% IO; **65–75% LTC for first-time builders, 70–80% for repeat builders** [S10]. A builder-finance channel quotes from 7.99% (capped near 10.99%), up to 90% LTC (100% with land subordination), 2% points [S38].
- **Bank/relationship spec lines** for experienced builders typically price closer to prime + 1–2% [A]; a first spec project should expect private/specialty pricing.
- Owner-occupied construction-to-perm rates (7.25–8.75%) [S25] do **not** apply to a build-for-sale.

Model: spec construction loan = **70% of the non-land project budget** (design/engineering, permits, utilities, hard, site, pool and the full 10% contingency); interest paid monthly (no reserve), IO on drawn funds, monthly S-curve draw schedule (average 50% outstanding during the 15-month build, 100% during the 3-month sale), **2% origination + $10K fees**; rate **8.5% (low) · 10.0% (base) · 11.5% (high)**. Seller-note interest accrues for all 27 months and is paid at the sale.

Leverage check (base case): the construction loan is ≈$1.92M; with the $2.5M note, combined debt (incl. $0.17M accrued note interest at 3%) is ≈$4.59M, **≈70% of the base sale value**, inside but near the top of the 65–75% completed-value caps in [S11, S37]. In the Worst case it is ≈84%, above a 75% cap, which would trim the loan by ≈$0.56M. In the Best case it is ≈58%. The subordination terms and the appraisal still decide whether a lender accepts the structure.

- **Hold alternative (one line):** refinancing the base case at completion into a 30-yr jumbo (80% of value, 7.50%) would retire the note and loan with ≈$0.63M to spare and cost ≈$36,499/mo P&I.


Land-terms reference: 6% vs. 0% at each case's costs. The cases now use 6% / 3% / 0% (Worst / Base / Best). For reference, this table shows each case at 6% and at 0% for three years (nothing down, all principal paid at the sale closing). The 27-month timeline fits inside a 3-year term with 9 months to spare; 0% requires the seller's agreement.

Land-terms scenario, 4,500 sf	Worst	Base	Best
Seller-note interest, 6% simple × 27 mo	$337,500	$337,500	$337,500
Seller-note interest, 0% for 3 years	$0	$0	$0
Total cost before sale, 6%	$6,554,720	$5,886,716	$5,281,812
Total cost before sale, 0%	$6,217,220	$5,549,216	$4,944,312
Net profit, 6%	−$0.71M	+$0.39M	+$1.43M
Net profit, 0%	−$0.37M	+$0.73M	+$1.77M
Margin on cost, 6% / 0%	−10.8% / −5.9%	+6.7% / +13.2%	+27.1% / +35.8%
Break-even sale $/sf, 6% / 0%	$1,513 / $1,435	$1,359 / $1,281	$1,219 / $1,142
Owner cash, either scenario	$1,441,870	$1,239,666	$1,037,462
Note payoff at sale, 6% / 0%	$2,837,500 / $2,500,000	same	same

- **What changes:** only the accrued note interest. Profit rises by $337,500 in every case, and break-even falls by ≈$77/sf. Owner cash is unchanged because the interest is deferred to the sale at any rate. Base at 3% sits halfway ($168,750).
- **If the timeline slips past month 36:** the note matures with the house unsold. The terms after maturity (extension options, default rate, or reversion to an interest rate) need to be in the note. Each month past 36 would cost ≈$12.5K at 6% (≈$6.25K at 3%); a maturity default on a subordinated note would also put the construction loan at risk.
- **Seller asks (flagged, not modelled):** 0% for three years is worth ≈$0.34M to the buyer at 6%, so the seller may ask for a higher price, a deposit, a shorter term, a personal guarantee, or resist subordination.

Construction loan interest: monthly draw schedule

Interest is charged only on money drawn, so the cost depends on how fast the budget is spent. The model draws the loan on a monthly schedule over the 15-month build and charges 10% on the outstanding balance each month (mid-month convention), then on the full balance for the 3-month sale. Base uses an **S-curve** (slow start for permits and foundations, fastest spend mid-build on framing, roof and MEP (mechanical, electrical, plumbing), tapering at finishes): the outstanding balance averages **50% of the loan** during the build.

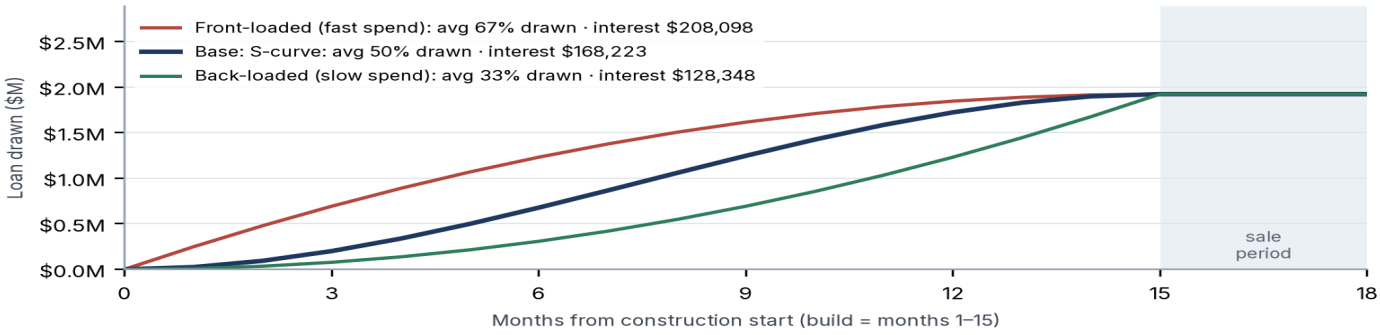

Cumulative loan drawn over the build for three draw speeds (Base-case loan)

How draw pace changes each case (case note rates 6% / 3% / 0%; cases use the S-curve)

Draw pace	Worst	Base	Best
Construction interest			
Front-loaded (fast spend)	$246,286	$208,098	$169,911
S-curve (case estimates)	$199,093	$168,223	$137,353
Back-loaded (slow spend)	$151,901	$128,348	$104,795
Net profit (margin on cost)			
Front-loaded (fast spend)	−$0.75M (−11.4%)	+$0.52M (+9.1%)	+$1.74M (+34.9%)
S-curve (case estimates)	−$0.71M (−10.8%)	+$0.56M (+9.8%)	+$1.77M (+35.8%)
Back-loaded (slow spend)	−$0.66M (−10.1%)	+$0.60M (+10.6%)	+$1.80M (+36.7%)

Takeaway: draw pace swings construction interest by about **±$40,000** around Base ($128,348–$208,098, a $79,750 range). Lenders usually require the owner's equity to go in first, which delays the loan draws and would lower interest further.

Curves: front-loaded = $1-(1-t)^2$, S-curve = $3t^2-2t^3$, back-loaded = t^2, where t is the share of the 15-month build elapsed; interest each month on the average balance outstanding that month, 10% interest-only; loan = 70% of the non-land budget. All case estimates in §6 use the S-curve.

C. Carry and cash flow by phase

Owner cash by phase, 4,500 sf

Phase	Worst	Base	Best	What it covers
Design & permit (months 1–9)	$283,344	$283,344	$283,344	Land closing, design/engineering, permits and utilities (counted toward the 30% equity), 9 months of tax and GL/flood
Construction (months 10–24)	$1,078,931	$887,404	$695,877	Loan closing, the rest of the 30% equity, construction interest, tax and insurance
Marketing & sale (months 25–27)	$79,594	$68,918	$58,241	Full construction-loan interest, tax and insurance
Total owner cash	**$1,441,870**	**$1,239,666**	**$1,037,463**	
At sale: net proceeds after repaying note and loan	+$0.74M	+$1.80M	+$2.81M	Sale price less sale costs, the $2.5M note with accrued interest ($337,500 / $168,750 / $0), and the construction loan; unspent contingency stays undrawn

Monthly carry, 4,500 sf

Phase	Worst	Base	Best	Components
Design & permit (months 1–9)	$3,844	$3,844	$3,844	Property tax ≈$3,010 + GL/flood ≈$833 (note interest accrues, not paid)
Construction (months 10–24), average	$17,051	$14,962	$12,873	+ construction interest (S-curve draws, avg 50% drawn) + builder's risk
Marketing & sale (months 25–27)	$26,531	$22,973	$19,414	Construction loan fully drawn + tax + insurance
Memo: seller-note interest (accrues; paid at sale)	$12,500	$6,250	$0	$2.5M × 6% / 3% / 0% ÷ 12; $337,500 / $168,750 / $0 over 27 months

Each month of delay during the build or sale costs ≈$13–39K: cash carry plus $0–12.5K of accruing note interest ($6.25K at Base 3%). Owner cash by item, the interest-reserve alternative and lender points are in §6 (Owner cash and monthly carry).

D. Build cost research and permit valuations

Source (2025–2026)	Published hard-cost range ($/sf of living area, excl. land)	Notes
Revolution Contractors, St. Pete (Apr 2026) [S1]	Custom in an AE/VE flood zone **$425–525**; waterfront Snell Isle / Shore Acres **$500–750**; ultra-custom waterfront **$700–1,000**	Flood-zone construction "at least 20%" over inland; elevation adds **$75K–200K+** vs. slab-on-grade (geotech $3–8K, piles $50–100K if needed, stem wall/flood vents $25–60K, elevated MEP $8–15K)
A2 Construction, Snell Isle (2026) [S3]	Elevated waterfront (canal/bayou) **$320–520**; open-bay estate **$520–640+**	Cost-plus pricing **before** the GC fee
St. Pete Home Guide, Snell Isle (Sep 2026) [S2]	Snell Isle Zone AE **$500–900** finished	AE elevation adds **$80–150K**; architecture 8–12% of hard cost
LaBram Homes, Tampa Bay [S6]	Coastal luxury **from $650+**	Builder marketing range
GGC Construction, Tampa Bay waterfront (2026) [S4]	Flood-zone site/foundation premium **$30–150K**	

City of St. Petersburg permit valuations (new single-family, 33704): declared construction values from the city's public permit layer [S22], matched to completed homes with known living area:

Address	Permit (year)	Declared value	Living area (sf)	Declared $/sf
105 Cordova Blvd NE	23-10001657	$2,165,000	7,640	$283
337 Coffee Pot Dr NE	24-2001363	$2,165,000	6,239	$347
1075 31st Ter NE	24-8000469	$1,200,000	6,774	$177
1695 Brightwaters Blvd NE	18-8000315 (built 2022)	$1,783,814	5,867	$304

Other recent (2025–2026) new-home permits in Snell Isle / Old NE carry declared values of **$1.2M–3.3M** (e.g., 300 Coffee Pot Riviera $3.0M, 411 Cordova $2.67M, 1501 Brightwaters $2.53M, 606 20th Ave NE $1.94M, 915 17th Ave NE $1.71M, 1218 Cordova $1.57M); living area for homes still under construction is not published. **Declared permit values run well below true cost** ($177–347/sf here vs. $425–750/sf in builder pricing) because they are owner/contractor declarations for fee purposes and typically exclude finishes, pool, site work and builder margin. They are a floor, not a budget.

Model inputs (hard cost, building only, elevation structure included): Worst $550 · Base $450 · Best $350 per sf of living area. The Best case sits at the low end of the A2 range ($320–520) and below the Revolution flood-zone floor ($425); it assumes a value-engineered design and competitive bids. Separately: site work/fill/elevation certificate $75K (elevated foundation assumed inside the $/sf) and pool/hardscape/landscape $160K, plus 10% contingency. The ≈8–8.7 ft floor raise is consistent with the "+20% / $75–200K" flood-zone premium in [S1]. The owner's team manages the build; a licensed GC qualifies the permit for **2% of hard cost** (in the pro forma) instead of a 10–20% cost-plus fee [S3].6M.

E. Tax and insurance assumptions

Item	Assumption	Basis
Property tax during the project	2026 just value $1,813,568 × 19.9197 mills ≈ **$36,126/yr (≈$3,010/mo)**; 27 months ≈ **$81,283**; land value only (no improvement value assumed before sale)	PCPAO; Pinellas 2025 millage [S13]
Builder's risk	**1.5%/yr** of the build budget for 18 months (build + sale)	Pinellas quotes $2.50–6.00 per $100 [S19]
General liability and flood (vacant lot / site)	**$10,000/yr** for 27 months	[A]
Deed doc stamps at sale	0.70% of price	[S9]
Note doc stamps / intangible tax	0.35% / 0.2% on the seller note and the construction loan	[S9]
Owner's title policy at sale	Florida promulgated rate	[S20]
Buyer's insurance (completed home)	Not in the pro forma; flood and wind premiums on a raised AE-zone home affect buyers' carrying cost and price	Quotes needed [S19]

F. Rate sensitivity: construction loan at 8.5% and 11.5% (4,500 sf)

Construction loan 8.5%

Hard $/sf ↓ · Sale $/sf →	$1,350	$1,450	$1,550	Break-even
$350	+$0.76M (+14.8%)	+$1.19M (+23.3%)	+$1.62M (+31.9%)	$1,176/sf
$450	+$0.16M (+2.7%)	+$0.59M (+10.3%)	+$1.02M (+18.0%)	$1,314/sf
$550	−$0.51M (−8.0%)	−$0.07M (−1.2%)	+$0.36M (+5.6%)	$1,467/sf

Construction loan 11.5%

Hard $/sf ↓ · Sale $/sf →	$1,350	$1,450	$1,550	Break-even
$350	+$0.71M (+13.9%)	+$1.15M (+22.4%)	+$1.58M (+30.8%)	$1,185/sf
$450	+$0.10M (+1.8%)	+$0.54M (+9.4%)	+$0.97M (+16.9%)	$1,326/sf
$550	−$0.57M (−8.9%)	−$0.13M (−2.1%)	+$0.30M (+4.7%)	$1,481/sf

Moving the loan rate from 8.5% to 11.5% shifts profit by ≈$40–60K in any cell; hard cost (≈$0.55M per $100/sf) and sale price (≈$0.43M per $100/sf) dominate.

G. Property, zoning, flood and city measurements

Property snapshot

Address / parcel	1500 N Shore Dr NE (PCPAO site address "15th Ave NE"), St. Petersburg, FL 33704 · parcel 17-31-17-83220-074-0120
Lot	≈14,160 sf (0.325 ac) per the 2023 Exacta boundary survey; PCPAO/GIS show 14,553 sf. Corner lot (15th Ave NE × N Shore Dr NE), trapezoidal, 15 ft alley along the north line
Zoning	NT-3. Legal front = 15th Ave NE. FAR 0.60 / building coverage 0.60 (one story); impervious cap 0.65 ≈ 9,200 sf (surveyed area)
Flood	FEMA AE, BFE 10 ft NAVD88; required finished floor ≈ 12 ft (BFE + 2 ft freeboard). Existing grade ≈ 3.3–4.3 ft. Small VE sliver at the SE corner, outside the buildable area
View / water	Park and Tampa Bay view across N Shore Dr. No water lot, seawall or dock
Land price (base)	**$2.50M** (base case for this pro forma). Last list price $2.65M (Feb 2026), shown for context only; the lot is off market ("hold" since Aug 19, 2026)
Land financing	Seller note [A]: **0% down**, $2.5M at 6% / 3% / 0% by case, interest accrued (≈$337,500 / $168,750 / $0) and paid with the principal at the home sale closing; must be **subordinated** to the construction lender
Construction financing	Spec construction loan: 70% of the non-land budget, interest-only on draws; 8.5–11.5% (base 10.0%), 2% fee
Strategy	**Spec build for sale**; benchmark 15–20% margin on cost; owner-managed build; GC qualifier fee 2% of hard cost
Product	Seller's courtyard design concept, scaled to 4,500 sf living area, finished floor raised to ≈12 ft
Base case (4,500 sf, $450/sf hard, $1,450/sf sale, 10% construction)	Total cost **$5.72M** · sale **$6.53M** · **net profit +$0.56M (+9.9% on cost)**; Worst −$0.71M, Best +$1.77M
Break-even / cash	Break-even sale **$1,142–1,513/sf** by case (Base $1,320/sf) · owner cash ≈**$1.04M–$1.44M** · cash carry ≈$4K/mo (design), ≈$13–18K/mo (build), ≈$19–26K/mo (sale period), plus $0–12.5K/mo of note interest accruing to the sale ($6.25K at Base 3%)

Location and lot notes

- **Location:** one of very few vacant lots on N Shore Dr NE, facing the waterfront park and Tampa Bay, walkable to downtown and the Vinoy. No other land sale on N Shore, Beach Dr or Bayshore was found for 2023–2026.
- **Lot quality:** large corner lot with alley access; not within a local historic district, so no design-review board applies.
- **Design head start:** the seller holds a 2023 boundary survey, a survey-based site plan and a landscape concept for a courtyard house by a licensed landscape architect.
- **Counterpoints:** no boat access; public park in front; flood zone AE and evacuation zone A; and the Base case needs a sale at $1,450/sf, near the top of the comp set, to earn +9.9% on cost (§6).

Seller's concept and scaling

What the seller's drawings show

- **Documents:** (1) Exacta Land Surveyors boundary survey #2212.3381 (field work Dec 29, 2022; signed Jan 2, 2023; boundary only, "not for construction"). (2) A proposed site plan on an older survey base (FEMA 2003 map, NAVD88) showing **finished floor 11.1 ft** and **roof peak 34′ 9½″ above grade**. (3) "Hardscape/Landscape Concept – Hudson," T.H. Davis, P.A., Landscape Architect (Clearwater), 1/8″ = 1′-0″.
- **Concept:** an L-shaped house wrapping a **central courtyard**; **pool and spa** within the courtyard/garden zone on the east side; **entry from 15th Ave NE** (the legal front) via a walk into the courtyard; **garage block on the alley (north) side**, reached from the alley; the **24″ oak at the NE corner kept**, with its root area protected in the landscape notes.
- **Size:** no floor plans or written square footage. Traced footprint ≈ **3,580 sf** (±150), of which the NW block (≈830 sf) appears to be the garage; ≈**2,750 sf of living area if one story**.

Scaling the concept to 4,500 sf living area

	Seller concept (traced)	Target
Living area (sf)	≈2,750 (if one story)	**4,500**
Added living area vs. concept	—	+1,750
How it fits	—	Partial second floor ≈1,750 sf, or a deeper one-story L
Finished floor	11.1 ft (pre-2021 map)	**≈12 ft** NAVD88
Garage	NW block, alley access	Alley block kept; at grade it is a flood-vented, non-habitable enclosure
FAR check (0.60 × 14,160 ≈ 8,500 sf)	Pass	Pass

- **Zoning envelope:** NT-3 setbacks; one-story coverage up to 0.60, impervious ≤ ≈9,200 sf (surveyed area); height measured from design flood elevation, so the ≈0.9 ft floor raise does not reduce the allowable envelope. The courtyard, pool deck and drive must be held within the impervious cap; pervious pavers or decking may be needed at the larger size.
- **Flood:** raising the floor from 11.1 to ≈12 ft adds roughly 0.9 ft to stem walls, entry stairs/ramps and courtyard grading; habitable space ≈8–8.7 ft above existing grade. Below-floor garage and storage must be flood-vented with a non-conversion agreement.
- **Pool barrier:** the courtyard walls and a 4 ft code barrier (FBC R4501.17) can double as privacy screening; front-yard (15th Ave) fence limits apply.
- **Trees:** the survey locates one 24″ oak (NE corner), which the concept keeps. Aerial imagery suggests additional canopy on the lot not shown on the boundary survey, so a **tree survey and arborist report** are required before design.
- **Design status:** the seller's material is a concept, not a permit set. A licensed architect must redraw it for current flood elevations and the larger program. The seller's architectural and CAD files should be requested.

Site and city measurements

Item	Value	Source
Parcel	17-31-17-83220-074-0120 · Snell & Hamlett's North Shore Add., Blk 74, Lot 11 less W 28 ft & all of Lot 12	PCPAO; Exacta survey
Surveyed boundary	North (15 ft alley) 162.87 ft · West 109.64 ft · South (15th Ave NE, 60 ft R/W) 95.09 ft · East (N Shore Dr NE, 70 ft R/W) 128.69 ft	Exacta #2212.3381, signed 1/2/2023
Area	0.325 ac ± ≈ 14,157 sf (survey) vs 14,552–14,553 sf (city GIS / PCPAO)	Survey; city GIS; PCPAO
City GIS parcel edges	South 96.3 ft · East 130.7 ft · West 111.2 ft · North 165.6 ft	City GIS parcels

Item	Value	Source
Zoning	NT-3 Neighborhood Traditional Single-Family; not in a local historic district (adjacent to the North Shore National Register district); legal front = 15th Ave NE	City zoning; LDR §16.20.010 [S39]
Grade	≈3.3–4.3 ft NAVD88	USGS 3DEP; seller site plan
NT-3 setbacks	Roofline ≤ 24 ft (one story)	Roofline > 24 ft
—	—	—
Front, building (15th Ave)	30 ft	40 ft
Front, open one-story porch	23 ft	40 ft
Interior side (west)	7.5 ft	16 ft
Street side (N Shore)	15 ft	22 ft
Rear with alley < 16 ft	10 ft, or 22 ft incl. alley width if less	20 ft
In-ground pool	≥ 5 ft from side, street-side and rear lines; not in the front yard	
Intensity cap	Ratio	On surveyed 14,157 sf
—	—	—:
FAR (base)	0.40	5,663
FAR max, all one-story (bonus +0.20)	0.60	8,494
Building coverage	0.55 (0.60 one story)	7,786 (8,494)
Impervious surface	0.65	**9,202**

Enclosed space below the design flood elevation is excluded from FAR. Building envelope after setbacks ≈7,970–8,430 sf (GIS basis). Height: 24 ft to roofline / 36 ft to peak, measured from the design flood elevation. **Design standards:** an identifiable architectural style is required ("Modern" is named in the code); corner lots need full architectural treatment on both street façades; an articulated base is required where the floor is 48″+ above grade; garage access from the alley [S39, S40].

Flood	Value
FEMA zone	**AE, BFE 10 ft NAVD88** on ≈14,046 sf; **VE, BFE 11** on ≈507 sf at the SE corner (inside the street-side setback). Panel 12103C0236H, eff. 8/24/2021
Required lowest floor	**≈12.0 ft NAVD88** (BFE + 2 ft city freeboard), ≈8–8.7 ft above grade
Seller's prior design	Finish floor 11.1 ft, drawn to the superseded 2003 map
Other	Evacuation zone A; no Coastal A / LiMWA mapped within 200 ft

City of St. Petersburg zoning (NT-3 tan · NSE green)



FEMA NFHL flood zones (panel 12103C0236H, eff. 8/24/2021)



Left: city zoning over Esri World Imagery with the parcel outline. Right: FEMA National Flood Hazard Layer zones and BFEs (rendered Oct 10, 2026).

H. Aerials, lot details and distances



Parcel aerial (Esri World Imagery) with the city GIS parcel outline

Lot details

- **Corner lot.** Frontage on 15th Ave NE (legal front, 95.09 ft) and N Shore Dr NE (128.69 ft), so both street façades are visible from the street.
- **Park and bay view.** Faces Flora Wylie Park, part of the waterfront park chain that runs from Vinoy Park through North Shore Park (pool and beach) to Coffee Pot Bayou, with Tampa Bay beyond. No water lot, seawall or dock.
- **Alley access.** A 15 ft alley runs along the 162.87 ft north line, so the garage, driveway and services can sit off the alley and keep both street frontages clean.
- **Mature oak.** A 24″ oak near the NE corner is kept in the seller's concept. Other trees and shrubs along the street edges are not located on the survey, so a tree survey is pending.
- **Flood zone.** FEMA AE (BFE 10 ft NAVD88) on ≈14,046 sf, plus a VE sliver of ≈507 sf at the SE corner that lies outside the building envelope. Finished floor ≈12 ft NAVD88, ≈8–8.7 ft above grade. Evacuation zone A.
- **NT-3 zoning.** Single-family, with a one-story building envelope of ≈7,970 sf after setbacks (city GIS basis) and FAR up to 0.60 for one story. The lot is not in a local historic district; it sits next to the North Shore National Register Historic District.
- **Survey.** Boundary survey, 2023 (Exacta #2212.3381); lines 95.09 / 128.69 / 109.64 / 162.87 ft.



Neighborhood aerial (Esri World Imagery): the lot, the North Shore waterfront parks, Coffee Pot Bayou, Snell Isle, the Vinoy, the Pier and downtown

Distances and times from the lot (all destinations)

#	Destination	Walk (route)	Drive (route, free-flow)	Straight line
1	Waterfront park across N Shore Dr NE (Flora Wylie Park)	0.04 mi · 1 min	0.04 mi · 1 min	0.04 mi
2	North Shore Park (901 N Shore Dr NE)	0.54 mi · 12 min	0.53 mi · 2 min	0.42 mi
3	North Shore Aquatic Complex	0.46 mi · 10 min	0.54 mi · 2 min	0.40 mi
4	The Vinoy Resort	0.83 mi · 18 min	0.86 mi · 3 min	0.69 mi
5	Beach Dr NE dining (at 3rd Ave NE)	1.05 mi · 22 min	1.09 mi · 4 min	0.99 mi
6	Museum of Fine Arts	1.06 mi · 23 min	1.09 mi · 4 min	0.98 mi
7	St. Pete Pier (Pier District entrance)	1.36 mi · 29 min	1.41 mi · 5 min	0.93 mi
8	The Dalí Museum	1.90 mi · 41 min	2.08 mi · 7 min	1.51 mi
9	Coffee Pot Park / Coffee Pot Bayou	1.32 mi · 28 min	1.48 mi · 5 min	1.09 mi
10	North Shore Elementary (200 35th Ave NE)	1.61 mi · 35 min	1.69 mi · 5 min	1.26 mi
11	Albert Whitted Airport	2.48 mi · 53 min	2.65 mi · 9 min	1.57 mi
12	Publix, 250 3rd St S (nearest by route)	1.69 mi · 36 min	1.79 mi · 6 min	1.43 mi
—	Tampa International Airport	—	20.6 mi · 33 min	14.2 mi

Walking and driving routes from OSRM on OpenStreetMap data (routing.openstreetmap.de foot profile; router.project-osrm.org car profile), computed Oct 10, 2026. Walking times assume ≈5 km/h; driving times are free-flow, without traffic or parking. Straight-line distance is shown for reference. Destination coordinates from OpenStreetMap and City of St. Petersburg GIS.



Aerial view (Google Maps satellite, Oct 2026). Corner of 15th Ave NE and N Shore Dr NE; North Shore Park to the east.




Esri World Imagery with the city GIS parcel outline (red) and a 10 ft grid (origin = SW corner). Tree positions approximate pending a tree survey.

I. Seller documents

EXACTA
Land Surveyors, LLC

www.exactaland.com | office: 866.735.1916 | fax: 866.744.2882



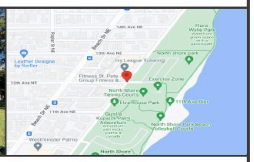

PROPERTY ADDRESS:
0 NORTH SHORE DRIVE NE, ST. PETERSBURG, FLORIDA 33704

SURVEY NUMBER: 2212.3381

DATE SIGNED: 01/02/23 | **FIELD WORK DATE:** 12/29/2022

REVISION DATE(S):
(REV.1 1/2/2023)

POINTS OF INTEREST
NONE VISIBLE

KENNETH L. WARD License Number LS 5646 STATE OF FLORIDA PROFESSIONAL SURVEYOR & MAPPER

KENNETH L. WARD
State of Florida Professional Surveyor and Mapper
License Number 5646
Exacta Land Surveyors, LLC | LB# 8291

SURVEYORS CERTIFICATE


I hereby certify that this Survey of the lands described hereon was made under my direct supervision, and to the best of my knowledge and belief is a true and accurate representation of said lands and meets the Standards of Practice set forth in Chapter 5J-15.050 through 5J -15.053, Florida Administrative Code, pursuant to section 472.027, Florida Statutes. This survey is not valid without the signature and original raised seal of a Florida licensed surveyor and mapper, except when the electronic signature and seal of a Florida licensed surveyor and mapper is affixed hereto.

EXACTA
Land Surveyors, LLC


Exacta Land Surveyors, LLC
LB# 8291
o: 866.735.1916 | f: 866.744.2882
3846 Blanding Boulevard, Jacksonville, FL 32210

Florida Land Title Association FLTA **AFFILIATE MEMBERS**

2212.3381
BOUNDARY SURVEY
PINELLAS COUNTY

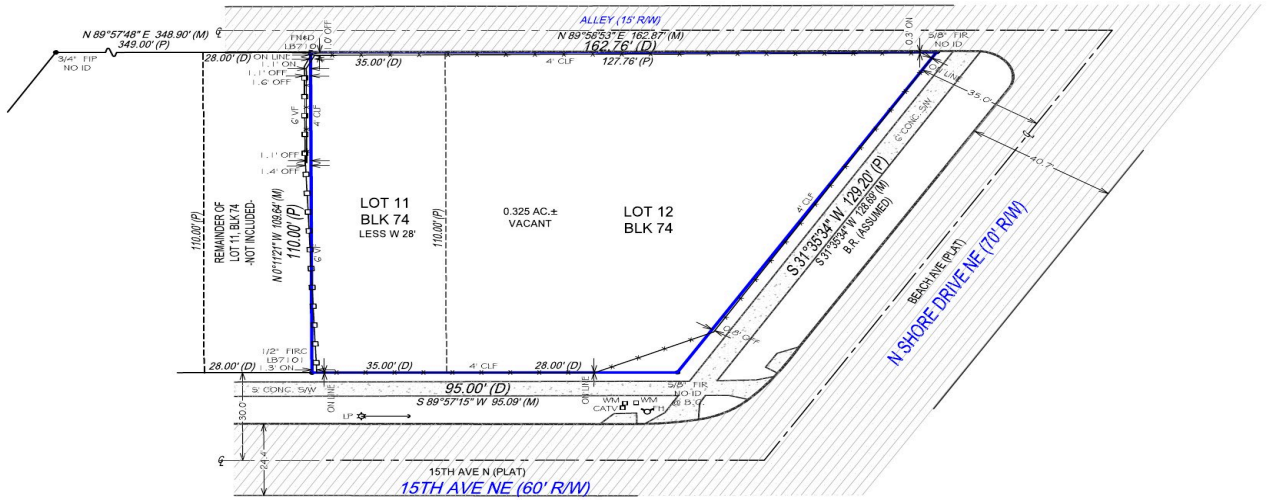

SURVEYOR'S NOTES:
FENCE OWNERSHIP NOT DETERMINED.

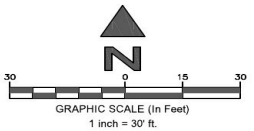

SEE PAGE 2 OF 2 FOR LEGAL DESCRIPTION
PAGE 1 OF 2 - NOT VALID WITHOUT ALL PAGES

Seller survey (Exacta Land Surveyors, #2212.3381, signed Jan 2, 2023), page 1 of 2.

PROPERTY ADDRESS:
0 NORTH SHORE DRIVE NE, ST. PETERSBURG, FLORIDA 33704

SURVEY NUMBER: 2212.3381

CERTIFIED TO:
GLORIA A HUDSON

DATE SIGNED: 01/02/23

BUYER: GLORIA A HUDSON.

LENDER: NOT PROVIDED

TITLE COMPANY: UNKNOWN

COMMITMENT DATE: NOT REVIEWED | **CLIENT FILE NO:**

LEGAL DESCRIPTION:
LOT 11, LESS THE WEST 28 FEET THEREOF AND ALL OF LOT 12, BLOCK 74, SNELL & HAMLETTS NORTH SHORE ADDITION, ACCORDING TO THE PLAT THEREOF, AS RECORDED IN PLAT BOOK 3, PAGE 40 OF THE PUBLIC RECORDS OF PINELLAS COUNTY, FLORIDA.

FLOOD ZONE INFORMATION:
BY PERFORMING A SEARCH WITH THE LOCAL GOVERNING MUNICIPALITY OR WWW.FEMA.GOV, THE PROPERTY APPEARS TO BE LOCATED IN ZONE AE AND VE (WITH A BASE FLOOD ELEVATION OF 11). THIS PROPERTY WAS FOUND IN THE CITY OF ST PETERSBURG, COMMUNITY NUMBER 125148, PANEL NUMBER 0236 DATED 08/24/2021.

GENERAL SURVEYORS NOTES:

1. The Legal Description used to perform this survey was supplied by others. This survey does not determine nor imply ownership of the lands or any fences shown hereon. Unless the Title Commitment Number is referenced on this survey, an examination of the abstract of title was NOT performed by the signing surveyor to determine which instruments, if any, are affecting this property.
2. The purpose of this survey is to establish the boundary of the lands described by the legal description provided and to depict the visible improvements thereon for a pending financial transaction. Underground footings, utilities, or other service lines, including roof eave overhangs were not located as part of this survey. Unless specifically stated otherwise the purpose and intent of this survey is not for any construction activities or future planning.
3. If there is a septic tank or drain field shown on this survey, the location depicted hereon was either shown to the surveyor by a third party or it was estimated by visual above ground inspection. No excavation was performed to determine its location.
4. This survey is exclusively for a pending financial transaction and only to be used by the parties to whom it is certified.
5. Alterations to this survey map and report by other than the signing surveyor are prohibited.
6. Dimensions are in feet and decimals thereof.
7. Any FEMA flood zone data contained on this survey is for informational purposes only. Research to obtain said data was performed at www.fema.gov and may not reflect the most recent information.
8. Unless otherwise noted "SIRC" indicates a Set Iron Rebar with a Cap stamped LB#8291, a minimum half inch in diameter and eighteen inches long.
9. If you are reading this survey in an electronic format, the information contained on this document is only valid if this document is electronically signed as specified in Chapter 5J17.062 (3) of the Florida Administrative Code and Florida Statute 472.025. The Electronic Signature File related to this document is prominently displayed on the invoice for this survey which is sent under separate cover. Manually signed and sealed logs of all survey signature files are kept in the office of the performing surveyor.
10. The symbols reflected in the legend and on this survey may have been enlarged or reduced for clarity. The symbols have been plotted at the approximate center of the field location and may not represent the actual shape or size of the feature.
11. Points of Interest (POI's) are select above-ground improvements, which may appear in conflict with boundary, building setback or easement lines, as defined by the parameters of this survey. These POI's may not represent all items of interest to the viewer. There may be additional POI's which are not shown or called-out as POI's, or which are otherwise unknown to the surveyor.
12. Utilities shown on the subject property may or may not indicate the existence of recorded or unrecorded utility easements.
13. The information contained on this survey has been performed exclusively by and is the sole responsibility of Exacta Land Surveyors, LLC. Additional logos or references to third party firms are for informational purposes only.
14. Pursuant to F.S. 558.0035, an individual employee or agent may not be held individually liable for negligence.
15. Due to varying construction standards, building dimensions are approximate and are not intended to be used for new construction or planning.

SURVEYORS LEGEND:

LINETYPES
- Boundary Line
- Center Line
- Chain Link or Wire Fence
- Easement
- Edge of Water
- Iron Fence
- Overhead Lines
- Structure
- Survey Tie Line
- Vinyl Fence
- Wall or Party Wall
- Wood Fence

SURFACE TYPES
- Asphalt
- Brick or Tile
- Concrete
- Covered Area
- Water
- Wood

SYMBOLS
- Benchmark
- Center Line
- Central Angle or Delta
- Common Ownership
- Control Point
- Catch Basin
- Elevation
- Fire Hydrant
- Find or Set Monument
- Guywire or Anchor
- Manhole
- Tree
- Utility or Light Pole
- Well


ABBREVIATIONS
(C) - Calculated
(D) - Deed
(F) - Field
(M) - Measured
(P) - Plat
(R) - Record
(S) - Survey
A/C - Air Conditioning
AE - Access Easement
ANE - Anchor Easement
ASBL - Accessory Setback Line
B/W - Bay/Box Window
BC - Block Corner
BFP - Backflow Preventer
BLDG - Building
BLK - Block
BM - Benchmark
BR - Bearing Reference
BRL - Building Restriction Line
BSMT - Basement
C - Curve
C/L - Center Line
C/P - Covered Porch
C/S - Concrete Slab
CATV - Cable TV Riser
CB - Concrete Block
CH - Chord Bearing
CHIM - Chimney
CLF - Chain Link Fence
CME - Canal Maintenance Easement
CO - Clean Out
CONC - Concrete
COR - Corner
CS/W - Concrete Sidewalk
CUE - Control Utility Easement
CVG - Concrete Valley Gutter
D/W - Driveway
DE - Drainage Easement
DF - Drain Field
DH - Drill Hole
DUE - Drainage & Utility Easement
ELEV - Elevation
EM - Electric Meter
ENCL - Enclosure
ENT - Entrance
EOP - Edge of Pavement
EOW - Edge of Water
ESMT - Easement
EUB - Electric Utility Box
F/DH - Found Drill Hole
FCM - Found Concrete Monument
FF - Finished Floor
FIP - Found Iron Pipe
FIPC - Found Iron Pipe & Cap
FIR - Found Iron Rod
FIRC - Found Iron Rod & Cap
FN - Found Nail
FN&D - Found Nail & Disc
FRRSPK - Found Rail Road Spike
GAR - Garage
GM - Gas Meter
ID - Identification
IE/EE - Ingress/Egress Easement
ILL - Illegible
INST - Instrument
INT - Intersection
IRRE - Irrigation Easement
L - Length
LAE - Limited Access Easement
LB# - License No. (Business)
LBE - Limited Buffer Easement
LE - Landscape Easement
LME - Lake/Landscape Maintenance Easement
LS# - License No. (Surveyor)
MB - Map Book
ME - Maintenance Easement
MES - Mitered End Section
MF - Metal Fence
MH - Manhole
MHWL - Mean High Water Line
NR - Non-Radial
NTS - Not to Scale
NAVD88 - North American Vertical Datum 1988
NGVD29 - National Geodetic Vertical Datum 1929
OG - On Ground
ORB - Official Records Book
ORV - Official Record Volume
O/A - Overall
O/S - Offset
OFF - Outside Subject Property
OH - Overhang
OHL - Overhead Utility Lines
OHWL - Ordinary High Water Line
ON - Inside Subject Property
P/E - Pool Equipment
PB - Plat Book
PC - Point of Curvature
PCC - Point of Compound Curvature
PCP - Permanent Control Point
PI - Point of Intersection
PLS - Professional Land Surveyor
PLT - Planter
POB - Point of Beginning
POC - Point of Commencement
PRC - Point of Reverse Curvature
PRM - Permanent Reference Monument
PSM - Professional Surveyor & Mapper
PT - Point of Tangency
PUE - Public Utility Easement
R - Radius or Radial
R/W - Right of Way
RES - Residential
RGE - Range
ROE - Roof Overhang Easement
RP - Radius Point
S/W - Sidewalk
SBL - Setback Line
SCL - Survey Closure Line
SCR - Screen
SEC - Section
SEP - Septic Tank
SEW - Sewer
SIRC - Set Iron Rod & Cap
SMWE - Storm Water Management Easement
SN&D - Set Nail and Disc
SQFT - Square Feet
STL - Survey Tie Line
STY - Story
SV - Sewer Valve
SWE - Sidewalk Easement
TBM - Temporary Bench Mark
TEL - Telephone Facilities
TOB - Top of Bank
TUE - Technological Utility Easement
TWP - Township
TX - Transformer
TYP - Typical
UE - Utility Easement
UG - Underground
UP - Utility Pole
UR - Utility Riser
VF - Vinyl Fence
W/C - Witness Corner
W/F - Water Filter
WF - Wood Fence
WM - Water Meter/Valve Box
WV - Water valve

JOB SPECIFIC SURVEYOR NOTES:
THE ASSUMED BEARING REFERENCE OF SOUTH 31 DEGREES 35 MINUTES 34 SECONDS WEST IS BASED ON THE WESTERLY RIGHT-OF-WAY LINE OF NORTH SHORE DRIVE NE, LOCATED WITHIN SNELL AND HAMLETTS NORTH SHORE ADDITION, ACCORDING TO THE PLAT THEREOF, AS RECORDED IN PLAT BOOK 3, PAGE 40 OF THE PUBLIC RECORDS OF PINELLAS COUNTY, FLORIDA.


EXACTA Land Surveyors, LLC
Exacta Land Surveyors, LLC
LB# 8291
o: 866.735.1916 | f: 866.744.2882
3846 Blanding Boulevard, Jacksonville, FL 32210

SEE PAGE 1 OF 2 FOR MAP OF PROPERTY
PAGE 2 OF 2 - NOT VALID WITHOUT ALL PAGES

Seller survey (Exacta, 2023), page 2 of 2: legal description, notes, legend, flood zone note.

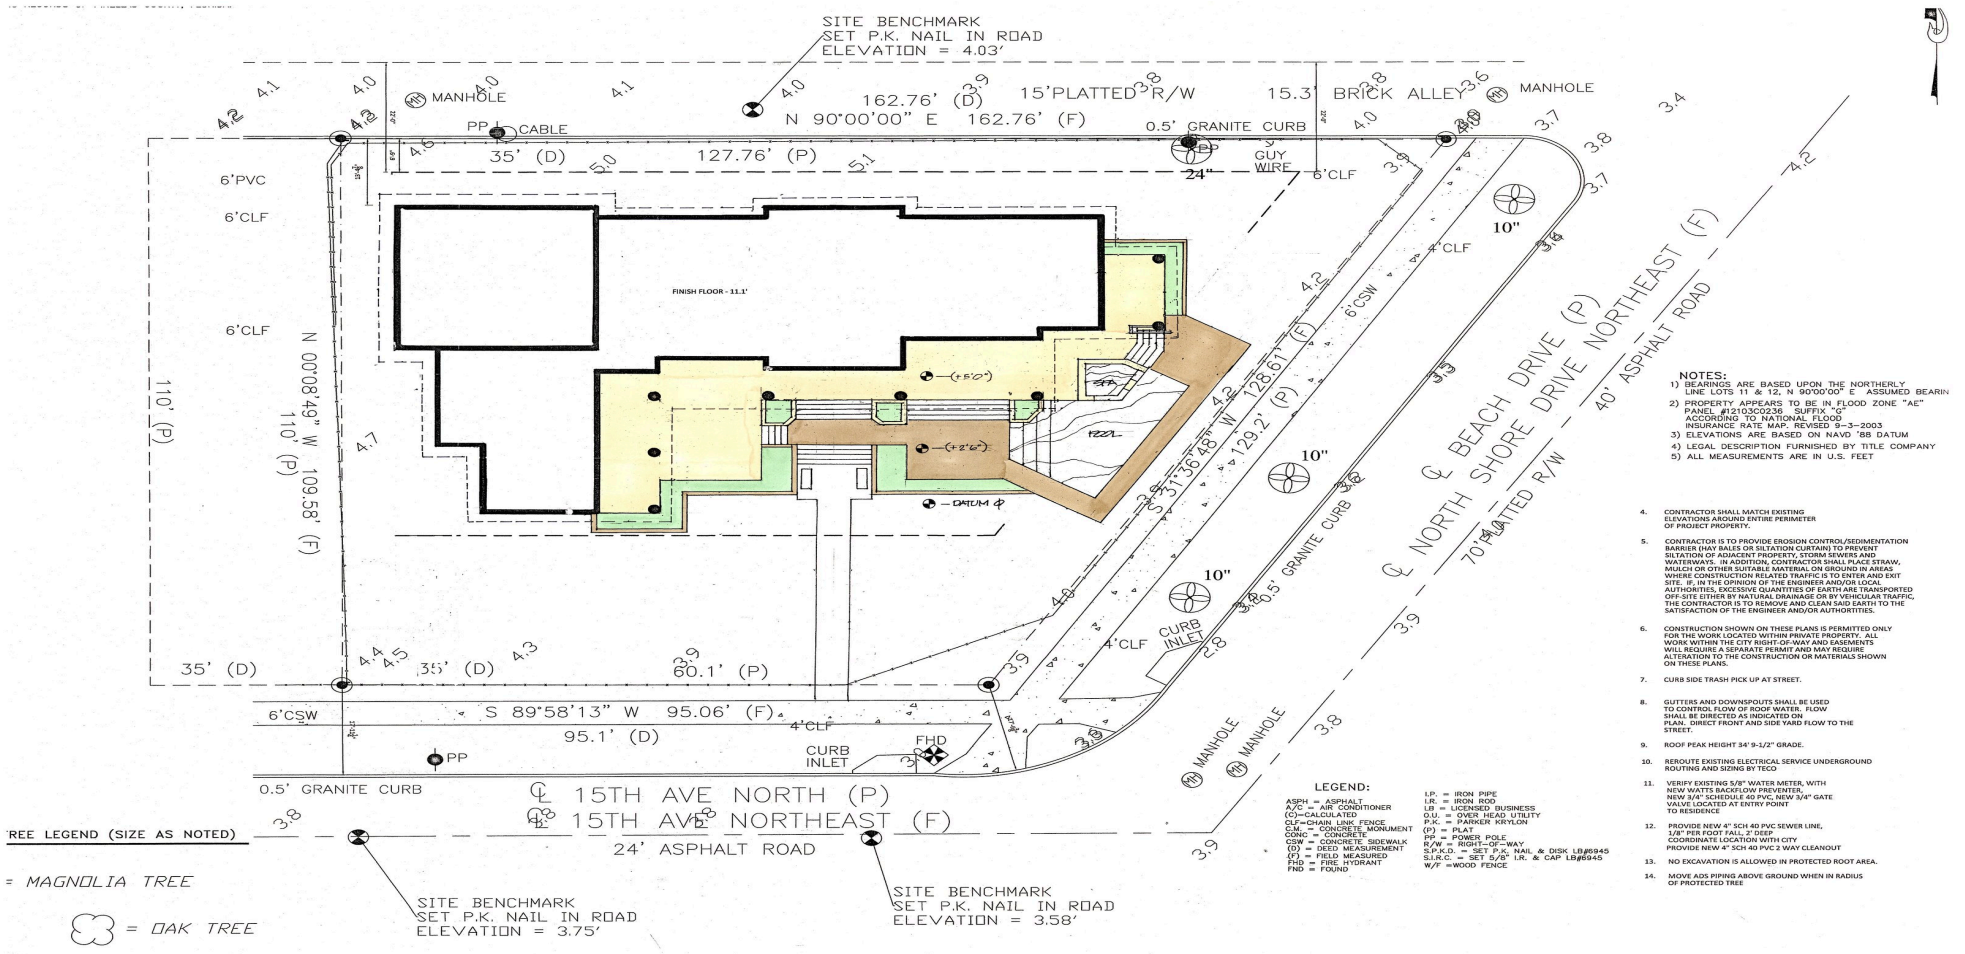

Seller site plan: courtyard design concept on a survey base (finished floor 11.1 ft; FEMA 2003 map). Traced footprint ≈3,580 sf.

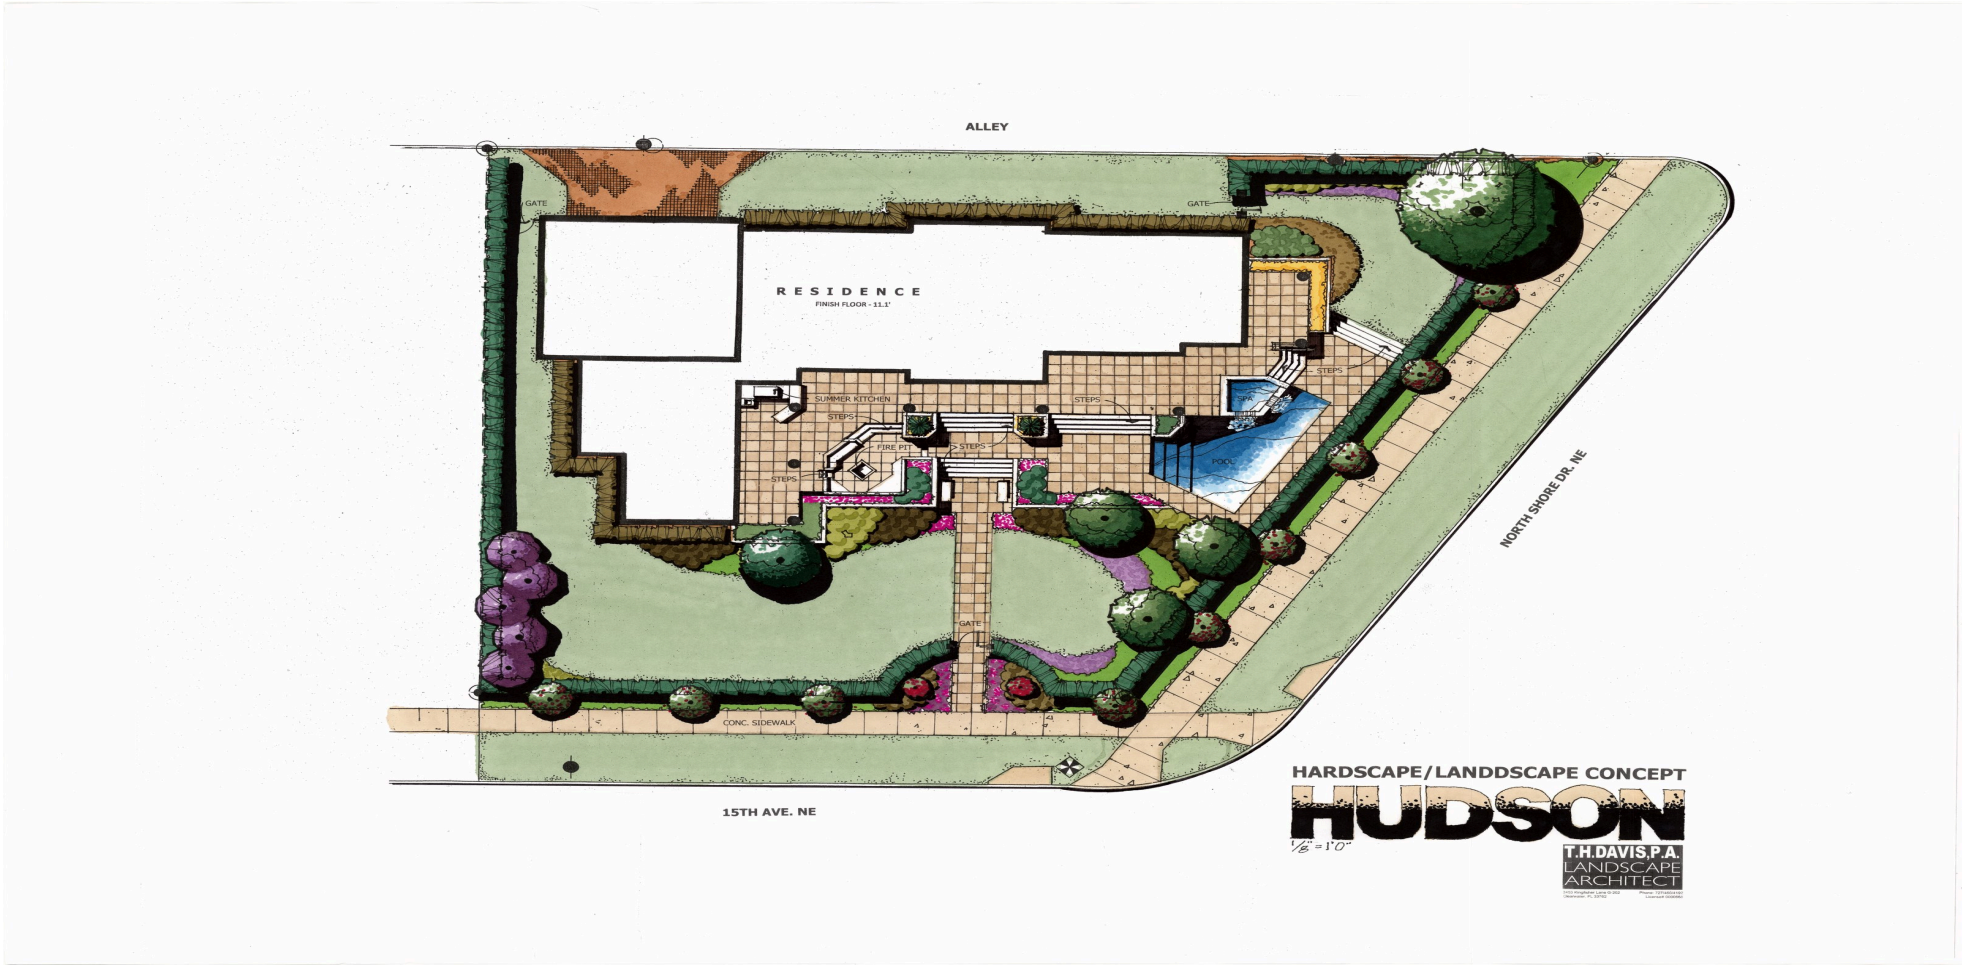

Hardscape/Landscape Concept – Hudson, T.H. Davis, P.A., Landscape Architect (seller design concept).

J. Listing agent comp sheet

1500 North Shore Drive NE
122 x 129 Size

Buyers will pay more for view + park + proximity to downtown + skyline view of downtown
North Shore Park is a 33-acres waterfront park with beach, playgrounds, dog park, aquatic complex, and sports courts connecting to the Vinoy Park and the downtown waterfront trail.

To many high-net-worth buyers, especially the ones driving the new ultra-luxury wave, boat access is secondary to lifestyle.

No seawall and exposure to the water impact insurance. Waterfront living without water ownership costs! Better use of a FRONT yard. The city maintains your front yard.

You are not buying dirt, you are buying the entire waterfront park system and walkable lifestyle to downtown. Those are GREAT buyers.

COMPS:

Not for Sale
1700 North Shore Drive NE
122 x 187 Lot Size
6,915 sqft built in 2017
PCPAO.org sale comparison - $7,704,100

Sarah SOLD
1800 North Shore Drive NE
101 x 217
4,527 sqft
Highest Sale in Old NE ever/ at the time
$6.1M in 3/2024
$1,350/sqft
Needed to be totally updated

Sarah SOLD
2030 Coffee Pot Blvd NE
87 x 145
6,076 sqft
Highest Sale in Old NE at this time
$7.15M 9/2025
$1,175/ sqft
Being completed renovated

Listing agent comp sheet, "1500 North Shore Drive NE" (Nov 19, 2025).

K. Full comps tables and high-end profiles

Combined home comps

One deduplicated table combining the research comps and the listing agent's comp sheet (Nov 2025). "Both" = appears in both sources. Price statistics use closed sales of 2015-or-newer waterfront homes plus 1800 N Shore, limited to homes of 6,000 sf living area or less (n = 5). 105 Cordova (7,640 sf), 1075 31st Ter (6,774 sf), 337 Coffee Pot Dr (6,239 sf) and 2030 Coffee Pot Blvd (6,076 sf) are listed but **excluded from the statistics** because larger homes carry lower $/sf; 1700 N Shore (6,915 sf) is a county model value, not a sale, and is shown for context only. Land comps are in §4 and Appendix K. The same set sets the expected sale price of the finished home.

Address	Sale date	Price	Living area (sf)	$/sf	Built	Age at sale	Water / dock	In stats	Source
1695 Brightwaters Blvd NE	2025-08-20	$8,800,000	5,867	$1,500	2022	3	0.55 ac; 147 ft open Tampa Bay frontage; dock w/ 2 lifts	yes	research
105 Cordova Blvd NE	2025-06-30	$8,800,000	7,640	$1,152	2024-25 (new)	0–1 (new)	0.5+ ac protected waterfront on Snell Isle Harbor; dock/lift	**no: >6,000 sf**	research
1075 31st Ter NE	2026-04-24	$7,950,000	6,774	$1,174	2026	0	0.35 ac; ~155 ft frontage, Smacks Bayou; 24,000-lb lift	**no: >6,000 sf**	research
2030 Coffee Pot Blvd NE	2025-09-16	$7,150,000	6,076	$1,177	2019	6	87×145 lot (20,072 sf); 2 deeded water lots on city seawall ACROSS the street, Coffee Pot Bayou	**no: >6,000 sf**	both
323 Cordova Blvd NE	2026-04-30	$6,750,000	4,657	$1,449	2020	6	98×185 lot (18,670 sf); Snell Isle Harbor; off-market sale	yes	research
337 Coffee Pot Dr NE	2026-09-28	$5,500,000	6,239	$882	2025	1	90×127 lot; dock across street; 90 ft bayou frontage (also sold 12/2025 for $5.6M)	**no: >6,000 sf**	research
1210 Monterey Blvd NE	2026-03-10	$4,850,000	4,560	$1,064	2016	10	80×160 lot; Coffee Pot Bayou; lift + floating dock	yes	research
301 Bayview Dr NE	2025-11-14	$4,000,000	4,087	$979	2015	10	79×138 lot + submerged land; Smacks Bayou/Tampa Bay; private dock	yes	research
1800 N Shore Dr NE	2024-03-22	$6,100,000	4,527	$1,347	1920	104	0.59 ac (101×217); 360 ft open waterfront via FOUR water lots across the park; dock/lift	yes	both
1237 Brightwaters Blvd NE	2026-04-27	$5,000,000	5,733	$872	1938	88	150×150 double lot; Tampa Bay; 20,000-lb lift	no	research
420 Coffee Pot Riviera NE	2026-04-16	$3,450,000	5,144	$671	1996	30	100×238 lot (0.5 ac); Coffee Pot Bayou; boat house	no	research
1323 Snell Harbor Dr NE	2026-02-17	$3,670,000	3,678	$998	1960	66	0.36 ac; ~89 ft frontage, open bay + Snell Isle Harbor; marketed as build-new site	no	research
1241 Snell Isle Blvd NE	2025-12-05	$3,050,000	3,387	$901	1965	60	19,820 sf lot; Snell Isle Harbor	no	research
2834 Coffee Pot Blvd NE	2025-07-31	$1,425,000	1,512	$942	1941	84	Coffee Pot Bayou; flooded, sold as-is for rebuild	no	research
214 Aranda St NE	2025-12-22	$3,550,000	4,741	$749	2025	0	10,549 sf lot; NOT waterfront (garden view)	no	research
1700 N Shore Dr NE	n/a (model value)	$7,704,100	6,915	$1,114	2017	n/a (not sold)	122×187 (0.47 ac); water lot/dock not confirmed	no	listing agent

- **Filtered set (n = 5, ≤ 6,000 sf) $/sf:** 979 · 1,064 · **1,347 (median)** · 1,449 · 1,500. Before the size filter (n = 9, incl. 337 Coffee Pot $882, 105 Cordova $1,152, 1075 31st Ter $1,174 and 2030 Coffee Pot $1,177): median $1,174, range $882–1,500. Pro forma sale cases: **Worst $1,350 · Base $1,450 · Best $1,550**.
- **Value at 4,500 sf:** $6.06M at the filtered median; $6.08M / $6.53M / $6.98M in the Worst / Base / Best cases.
- **The listing agent's $7M guidance:** at 4,500 sf, $7M implies $1,556/sf, above every sale in the set; the only sales at $1,449–1,500/sf have direct harbor or open-bay frontage with docks, which 1500 N Shore lacks. The $7M+ sales (2030 Coffee Pot, 105 Cordova, 1695 Brightwaters, 1075 31st Ter) reach that price through **size (5,900–7,600 sf)**, not higher $/sf. At $1,347–1,500/sf, $7M implies ≈4,700–5,200 sf living area.
- **In the lot's favor:** 1700 N Shore (same street, built 2017) carries a $7.7M county model value; the park, bay view and walk to downtown are real draws that waterfront-heavy comps may undercount.

Land / teardown comps

Group	Address	Sold	Price	Lot sf	$/sf total	$/sf upland	Flood	Notes
A direct seawall	1323 Snell Harbor Dr NE	2026-02-17	$3,670,000	15,991	$230		flood insurance required (zone not shown)	1960 house, marketed as build-new site; open bay + Snell Isle Harbor; dock w/ 10k lift
A direct seawall	1026 Monterey Blvd NE	2023-02-13	$1,900,000	13,482	$141		AE	Coffee Pot Bayou, riprap, composite dock; now unimproved; relisted $2.1-2.7M since Nov 2023 without selling (active $2.3M). Improved/vacant status at 2023 sale not confirmed
A direct seawall	490 Coffee Pot Riviera NE	2025-02-10	$2,000,000	16,988	$118		not shown	Helene-flooded 1952 house sold as-is for land value; new composite dock; Coffee Pot Bayou
A direct seawall (unconfirmed land sale)	1241 Snell Isle Blvd NE	2025-12-05	$3,050,000	19,820	$154		not shown	1965 house, off-MLS 'sold data entry only'; Snell Isle Harbor; land-value status NOT confirmed
B deeded water lot across street	2834 Coffee Pot Blvd NE	2025-07-31	$1,425,000	17,006	$84	$189	not shown (flooded)	1941 flooded house sold as-is to rebuild; upland sf computed from dims; 66 ft = lot width proxy
B deeded water lot across street	2800 Coffee Pot Blvd NE	2026-07-09	$1,450,000	17,990	$81	$164	AE	Helene-flooded 1951 house, land+dock value; listed $1.6M; 69 waterfront ft

Group	Address	Sold	Price	Lot sf	$/sf total	$/sf upland	Flood	Notes
B deeded water lot across street	2310 Coffee Pot Blvd NE	2025-06-24	$1,100,000	10,311	$107	$147	AE	Vacant lot, Granada Terrace historic district; listed $1.75M
C across-street view, NO water lot	1956 Coffee Pot Blvd NE	2026-08-12 (deed) / 2026-08-17 (MLS)	$2,800,000	14,588	$192	$192	AE	PCPAO: vacant, Seawall No, view Canal/River, legal Blk 66 Lot 5 only (no water lot), no dock. Listed $2.5M May 2026, sold over ask; earlier listings $2.9-3.2M expired 2024-26
D interior	255 19th Ave NE (Old NE)	2026-10-02	$1,225,000	8,799	$139		X	sold strictly for land value (teardown); also sold 2/12/2025 for $1,053,500 per public record
D interior	105 20th Ave NE (Old NE)	2024-11-26	$865,000	7,700	$112		X	vacant corner lot, alley
D interior	TBD 22nd Ave N (Old NE)	2024-12-05	$525,000	5,031	$104		not shown (non-evac zone)	vacant cleared lot
D interior	300 Rafael Blvd NE (Snell Isle)	2026-06-30	$2,200,000	28,440	$77		not shown	vacant, Vinoy golf view
D interior	1101 Snell Isle Blvd NE	2026-05-08	$875,000	14,196	$62		AE	vacant
D interior	827 Snell Isle Blvd NE	2026-02-13	$630,000	11,426	$55		not shown	sold as land value only
D interior	505 Snell Isle Blvd NE	2026-08-10	$450,000	7,256	$62		not shown	vacant, golf view
D interior	515 Snell Isle Blvd NE	2026-09-18	$500,000	7,573	$66		not shown	vacant, golf view

High-end comp profiles

The six highest closed sales by price or $/sf in Old Northeast and Snell Isle over 2024–2026. Photos are public listing images (MLS via BEX Realty).

1695 Brightwaters Blvd NE (Snell Isle)



1695 Brightwaters Blvd NE (Snell Isle)

- **Sale:** Sold Aug 20, 2025 · **$8.80M** · 5,867 sf · **$1,500/sf** · built 2022 (Windstar Homes)
- **Lot / water:** 0.55 ac (132×185); 147 ft open Tampa Bay frontage; dock with 2 lifts
- **Design:** Coastal / Florida-vernacular, two stories; white board-and-batten gables, **standing-seam metal roof**, block construction; raised entry with a wide stair; gunite pool, outdoor kitchen and shower, balcony; open-bay views

323 Cordova Blvd NE (Snell Isle)



323 Cordova Blvd NE (Snell Isle)

- **Sale:** Sold Apr 30, 2026 (off market) · **$6.75M** · 4,657 sf · **$1,449/sf** · built 2020 (Paragon Waterfront Homes)
- **Lot / water:** 98×185 (18,670 sf); Snell Isle Harbor
- **Design:** Low-slung **modern**: flat membrane roofs, block and smooth stucco, floor-to-ceiling glass; saltwater **infinity pool** with heater, outdoor kitchen, permeable paving. Closest in size to the 4,500 sf target

1800 N Shore Dr NE (Old Northeast)



1800 N Shore Dr NE (Old Northeast)

- **Sale:** Sold Mar 22, 2024 · **$6.10M** · 4,527 sf · **$1,347/sf** · built 1920; listing agent's sale ("highest sale in Old NE at the time")
- **Lot / water:** Corner, 0.59 ac (101×217); 360 ft of open-bay frontage via four water lots across the park; dock/lift
- **Design: Palm Beach / Mediterranean Revival**: white stucco and brick, **green barrel-tile roof**, columned entry; infinity pool, multiple porches. Same street and same park/bay outlook as the subject; needed full updating

2030 Coffee Pot Blvd NE (Old Northeast) †



2030 Coffee Pot Blvd NE (Old Northeast)

- **Sale:** Sold Sep 16, 2025 · **$7.15M** · 6,076 sf · **$1,177/sf** · built 2019; listing agent's sale
- **Lot / water:** 87×145 lot; two deeded water lots on the city seawall across the street (Coffee Pot Bayou)
- **Design: West Indies-inspired**: tile roof, block and stucco, deep **wrap-around porches** on two levels, elevator; **courtyard-style pool** and patio with outdoor kitchen; bayou views over the street. Closest analogue to the seller's courtyard concept


105 Cordova Blvd NE (Snell Isle) †



105 Cordova Blvd NE (Snell Isle)

- **Sale:** Sold Jun 30, 2025 · **$8.80M** · 7,640 sf · **$1,152/sf** · built 2024–25 (Don Hughes)
- **Lot / water:** 88×228 (22,595 sf); Snell Isle Harbor; dock/lift
- **Design: Coastal contemporary**, two stories: tile roof, block and stucco, large glazing, motor court; saltwater infinity pool with heater, outdoor kitchen, elevator; sold after price reductions

1075 31st Ter NE (Snell Isle Estates) †

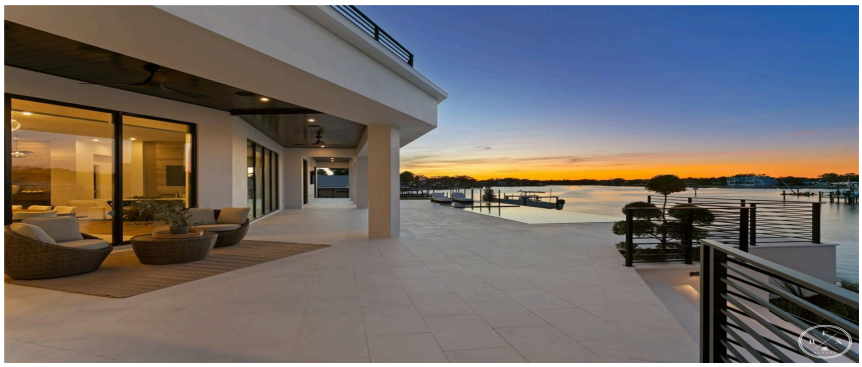

1075 31st Ter NE (Snell Isle Estates)

- **Sale:** Sold Apr 24, 2026 · **$7.95M** · 6,774 sf · **$1,174/sf** · built 2026 (Paragon Waterfront Homes)
- **Lot / water:** 121×146 (0.35 ac); ≈155 ft on Smacks Bayou; 24,000-lb lift
- **Design: Contemporary coastal**: block, brick and stucco, glass rail terraces, wrap-around screened porch; saltwater pool with heater, outdoor kitchen; sunset water views from the terrace (photo)

1700 N Shore Dr NE (6,915 sf, built 2017; county model value $7.70M, $1,114/sf) has not sold since 2015 and no public photo was retrievable, so it is not profiled.

What defines the top of this market

1. **Water access sets the $/sf ceiling.** Every sale above $1,350/sf has direct open-bay or harbor frontage with a dock (1695 Brightwaters, 323 Cordova) or extensive deeded water lots with a dock (1800 N Shore). View-only and across-the-street water lots trade at ≈$1,150–1,180/sf.
2. **Size drives the $7M+ prices.** $7M+ sales are 5,900–7,600 sf at $1,150–1,500/sf; 4,500–4,700 sf homes top out at $6.1–6.75M.
3. **Newer is required, style is not.** Winning designs range from modern (323 Cordova) to coastal vernacular (1695 Brightwaters) to West Indies (2030 Coffee Pot) and restored Palm Beach (1800 N Shore). The common thread is CBS/block-and-stucco construction, a premium roof (tile or standing-seam metal), and large glazing toward the water.
4. **Outdoor living is standard.** Saltwater or infinity pools with heaters, outdoor kitchens, covered terraces and courtyards appear in all six; the seller's courtyard-and-pool concept fits this pattern.
5. **Elevation is expected.** Recent builds sit on raised floors with grand entry stairs; the ≈8 ft raise at 1500 N Shore is in line with the market, not a handicap.
6. **Soft spots:** large price cuts at 105 Cordova and 337 Coffee Pot show depth is thin above $7M.

L. Risks, timeline and open questions

Key risks and diligence

- **Subordination:** the base case depends on the seller subordinating the note through the sale. Without it, the construction loan must retire the note, roughly $1M+ more cash is needed, and few spec lenders finance land plus vertical at this size.
- **Spec financing:** combined debt (note + loan) is ≈58–84% of value across the cases, against 65–75% completed-value caps; a first-time spec borrower should expect 65–75% LTC and private pricing (≈10–11.5%).
- **Note term:** the note must run at least 27–33 months (design, build, sale), with extension rights if the sale is slow.
- **Survey and trees:** order topo, elevations and a tree survey; confirm the VE line, the 15 ft alley and the 14,160 vs. 14,553 sf discrepancy. Arborist report on the NE oak and any other protected trees.
- **Zoning determinations:** front façade and entry (15th Ave), pool placement, alley rear setback, impervious treatment of the courtyard and pool.
- **Flood and insurance:** confirm freeboard and datum; obtain builder's risk, flood and wind quotes; buyers will underwrite the completed-home flood/wind premium [S19].
- **Build cost:** builder-published ranges, not bids; obtain 2–3 trade-level budgets on a schematic and a signed qualifier agreement.
- **Market / absorption:** the buyer pool above $5M is thin (price cuts at 105 Cordova and 337 Coffee Pot); each extra month on market costs ≈$26–33K at Base, including $6.25K of accruing note interest at 3%.
- **Licensing:** a spec build requires a licensed general contractor (owner-builder status is not available for a home built for sale, Fla. Stat. §489.103(7)); the model carries a 2% qualifier fee, and the qualifier must genuinely supervise the work (§489.1195) [S44].

Timeline [A]

Phase	Months
Due diligence and contract (survey, arborist, zoning letters, GC budget, loan pre-approval)	1–2 (before closing)
Design and permitting (architect, engineering; flood and tree review); seller-note interest accrues	6–12 (base 9)
Spec construction loan closes (seller note subordinated, stays in place)	≈month 9
Construction, including pool (IO on draws)	12–18 (base 15)
Certificate of occupancy; marketing	≈month 24 (range 18–30)
Sale closes; note and loan repaid from proceeds	≈month 27 (range 20–34)

Open questions and next steps

1. **Seller:** 0%-down note through sale, interest deferred to the sale (or 0% for 3 years), **subordination to the construction lender**, term ≥27–33 months with extensions, prepayment at sale; delivery of the architectural/CAD files for the courtyard concept.
2. **Lenders:** spec construction term sheets (rate, LTC, completed-value cap, treatment of a subordinated seller note, recourse).
3. **Listing agent:** basis for $7M; any water rights or dock at 1700 N Shore.
4. **Owner decisions:** go/no-go against the 15–20% benchmark; cash commitment (≈$1.24M in the Base case; $1.04M–$1.44M across cases).
5. **Bids and quotes:** 2–3 GC budgets with fee; builder's risk, flood and wind quotes.
6. **City:** pre-application meeting with St. Petersburg Zoning (front, pool, alley, impervious).

M. Path to $350/sf: line-item budget and levers

Scope. Hard cost for the building only, 4,500 sf of living area on one living level raised to ≈12 ft NAVD88 over a ground-level garage and parking, flood zone AE. Excluded and carried elsewhere in the pro forma: pool, hardscape and landscape ($160K), site work and fill ($75K), design and engineering, permits and impact fees, builder's risk and GL insurance, and the 10% contingency. **GC qualifier fee** (2% of hard cost) is in the §6 pro forma, not in this number. All allocations are **estimates**; category shares are benchmarked to NAHB's 2024 Cost of Constructing a Home survey [N1] (national average: foundations 10.5%, framing 16.6%, exterior finishes 13.4%, major systems 19.2%, interior finishes 24.1%) and adjusted for elevated construction, Florida impact glazing and an elevator.

Line item · 4,500 sf living area, building only	$350/sf · path case			$450/sf · Base			$550/sf · Worst		
	$	$/sf	%	$	$/sf	%	$	$/sf	%
FOUNDATION & ELEVATION									
Foundation & elevation: footings or piles, ground slab, columns/walls, elevated structural slab, flood vents	$225,000	$50	14.3%	$245,000	$54	12.1%	$275,000	$61	11.1%
STRUCTURE & ENVELOPE									
Structure & roof framing: CMU ground level, main level walls, trusses, sheathing, straps	$205,000	$46	13.0%	$235,000	$52	11.6%	$265,000	$59	10.7%
Roofing	$70,000	$16	4.4%	$90,000	$20	4.4%	$115,000	$26	4.6%
Windows & exterior doors, impact-rated	$120,000	$27	7.6%	$165,000	$37	8.1%	$215,000	$48	8.7%
Exterior finishes: stucco, soffits, trim, exterior paint	$80,000	$18	5.1%	$100,000	$22	4.9%	$115,000	$26	4.6%
MEP									
HVAC (2–3 zoned systems, ductwork, ERV)	$60,000	$13	3.8%	$75,000	$17	3.7%	$95,000	$21	3.8%
Plumbing rough-in & water heating	$55,000	$12	3.5%	$68,000	$15	3.4%	$82,000	$18	3.3%
Electrical rough-in, service, low-voltage	$62,000	$14	3.9%	$80,000	$18	4.0%	$100,000	$22	4.0%
Standby generator (whole-house)	$20,000	$4	1.3%	$26,000	$6	1.3%	$35,000	$8	1.4%
Elevator, 2-stop (garage to main level)	$40,000	$9	2.5%	$48,000	$11	2.4%	$60,000	$13	2.4%
INTERIOR SHELL									
Insulation (spray foam at roof deck + batts)	$28,000	$6	1.8%	$35,000	$8	1.7%	$42,000	$9	1.7%
Drywall	$52,000	$12	3.3%	$62,000	$14	3.1%	$75,000	$17	3.0%
INTERIOR FINISHES									
Flooring	$68,000	$15	4.3%	$92,000	$20	4.5%	$110,000	$24	4.4%
Tile (baths, showers, backsplash)	$42,000	$9	2.7%	$58,000	$13	2.9%	$78,000	$17	3.2%
Interior paint	$28,000	$6	1.8%	$35,000	$8	1.7%	$42,000	$9	1.7%
Trim, interior doors, hardware	$42,000	$9	2.7%	$62,000	$14	3.1%	$77,000	$17	3.1%
KITCHEN, BATHS & FIXTURES									
Cabinetry & millwork	$95,000	$21	6.0%	$140,000	$31	6.9%	$175,000	$39	7.1%
Countertops	$34,000	$8	2.2%	$50,000	$11	2.5%	$70,000	$16	2.8%
Appliances	$32,000	$7	2.0%	$55,000	$12	2.7%	$75,000	$17	3.0%
Plumbing fixtures	$28,000	$6	1.8%	$42,000	$9	2.1%	$57,000	$13	2.3%
Lighting fixtures	$18,000	$4	1.1%	$30,000	$7	1.5%	$40,000	$9	1.6%
Shower glass, mirrors, closets, specialties	$18,000	$4	1.1%	$28,000	$6	1.4%	$38,000	$8	1.5%
STAIRS & GARAGE									
Stairs & railings (entry stair + interior)	$32,000	$7	2.0%	$48,000	$11	2.4%	$60,000	$13	2.4%
Garage: overhead doors, flood-resistant finishes, epoxy, rated ceiling	$22,000	$5	1.4%	$27,000	$6	1.3%	$32,000	$7	1.3%
Testing, special inspections, trade permits	$8,000	$2	0.5%	$10,000	$2	0.5%	$12,000	$3	0.5%
GENERAL CONDITIONS									
General conditions: site supervision, dumpsters, temp utilities, cleaning, equipment	$91,000	$20	5.8%	$119,000	$26	5.9%	$135,000	$30	5.5%
Total hard cost, building only	**$1,575,000**	**$350**	**100%**	**$2,025,000**	**$450**	**100%**	**$2,475,000**	**$550**	**100%**

What the $350/sf column assumes, line by line

Line item	What $350/sf buys	Basis
Foundation & elevation	Geotech-led: spread footings on compacted fill if soils allow; CMU ground level with garage; elevated slab	NAHB foundations 10.5% (on-grade) [N1]; elevation premium $75–200K [S1]; piles $50–100K if required [S1]
Structure & roof framing	Rectangular footprint, one roof form, engineered trusses, standard 10 ft plate	NAHB framing 16.6% [N1]; est.
Roofing	Standing seam on a simple hip or gable (~5,200 sf with overhangs); membrane on flat sections	NAHB roofing 3.9% [N1]; est. (standing seam > tile on cost in most local bids)
Windows & exterior doors, impact-rated	~1,100 sf of openings, value-tier aluminum impact, standard sizes, 8–12 ft sliders; fiberglass entry door	FL impact $55–140/sf installed; sliders $80–200/sf; pivot doors $5–12K+ [N2, N3]
Exterior finishes	Smooth stucco, one accent material at entry only	NAHB exterior wall finish 5.7% [N1]; est.
HVAC (2–3 zoned systems, ductwork, ERV)	High-SEER split systems, no VRF	NAHB HVAC 6.3% [N1]; est.
Plumbing rough-in & water heating	PEX, tankless gas, stacked wet walls	NAHB plumbing 6.3% [N1]; est.
Electrical rough-in, service, low-voltage	400A service, prewire for AV/security, standard devices	NAHB electrical 6.4% [N1]; est.
Standby generator (whole-house)	24–26 kW air-cooled, gas, auto transfer	Est. (local installer quotes not obtained)
Elevator, 2-stop (garage to main level)	Basic hydraulic or MRL cab; shaft framed in structure	FL 2-stop hydraulic $25–55K; firm FL quote $29.5K excl. hoistway [N4, N5]
Insulation (spray foam at roof deck + batts)	Open-cell at roof deck, batts at walls	NAHB insulation 1.6% [N1]; est.
Drywall	Level 4 smooth, minimal soffits/coffers	NAHB drywall 3.3% [N1]; est.
Flooring	Large-format porcelain or engineered oak, one material throughout	NAHB flooring 3.6% [N1]; est.
Tile (baths, showers, backsplash)	Porcelain; stone at primary bath only	Est.
Interior paint	Two-color scheme	NAHB painting 2.6% [N1]; est.

Line item	What $350/sf buys	Basis
Trim, interior doors, hardware	Flat-stock trim, 8 ft solid-core doors, mid-tier hardware	NAHB trim/doors 3.0% [N1]; est.
Cabinetry & millwork	Semi-custom flat-panel; custom only in kitchen island and primary bath	NAHB cabinets + counters 4.5% [N1]; est.
Countertops	Quartz throughout; quartzite at kitchen island	Est.
Appliances	Pro-style package (e.g., Café/Monogram tier), panel-ready fridge	NAHB appliances 1.8% [N1]; est.
Plumbing fixtures	Mid-luxury brand, one statement tub	NAHB plumbing fixtures 1.9% [N1]; est.
Lighting fixtures	Recessed + 4–6 statement fixtures	NAHB lighting 1.3% [N1]; est.
Shower glass, mirrors, closets, specialties	Frameless glass, wire/laminate closet systems	Est.
Stairs & railings (entry stair + interior)	Concrete entry stair with stucco walls; simple metal rail	Est.
Garage	Insulated steel doors, epoxy floor	Est.
Testing, special inspections, trade permits	Main permit and impact fees are in soft costs ($40K)	Est.; permits & impact fees carried in soft costs
General conditions	Owner-managed with a paid site superintendent; insurance carried separately	Est.; builder's risk/GL in carry line; GC qualifier fee in the pro forma

Levers (savings measured against the $450/sf Base budget; ranges overlap and are not additive; the gap from $450 to $350 is $450K)

Lever	What it means	Savings vs. $450 Base	Note
Spec-level finishes with targeted splurges	Spend in the kitchen, primary bath, entry and the view wall; standardize everything else (cabinets, counters, appliances, flooring, tile, trim, fixtures, lighting).	≈$150–220K	Largest single lever: the $450→$350 finish lines differ by ≈$192K
Simple massing and a value-engineered plan	Rectangular footprint, minimal corners, one roof form, stacked plumbing, standard spans; a repeat or design-build plan reviewed for cost before permit.	≈$70–140K	Structure, roof, exterior, drywall and MEP runs
Direct trade buying and competitive bids	Three or more bids per trade; buy appliances, tile, fixtures, lighting and windows direct at trade pricing.	≈$60–120K	5–8% of trade and material cost; overlaps with the other levers
Glass strategy	Hold openings to ≈1,100 sf in standard sizes; 8–12 ft sliders instead of pivot or multi-slide pocket walls; value-tier impact line.	≈$40–90K	Impact glazing runs $55–140/sf installed [N2]
Foundation choice for the 8 ft raise	Geotech first: spread footings on compacted fill vs. piles; CMU ground level with garage vs. structural columns; precast or filigree elevated deck vs. cast-in-place.	≈$30–80K	Soils-dependent; piles alone run $50–100K [S1]
Owner-managed general conditions	Owner-managed build with one paid site superintendent and lean temporary facilities.	≈$25–50K	A full GC fee (10–20%) is already replaced by the 2% qualifier fee
Timing	Bid in the slower season; order windows, roofing and the elevator early; dry-in before peak hurricane season.	≈$15–40K	Mostly avoided cost and schedule risk
Skip the elevator (not recommended)	Stairs only, with a shaft-ready stacked closet ($5–8K).	≈$35–45K	An ≈8 ft climb to every room is a resale risk at $6M+

Elevator flag. With the main living level ≈8 ft above the garage, a stairs-only plan means a full flight for every arrival, grocery run and guest. At $6M+, where many buyers are downsizers, that is likely to narrow the buyer pool; the $350/sf column therefore keeps a basic 2-stop elevator (≈$40K; FL 2-stop hydraulic $25–55K [N4, N5]).

Net profit (margin on cost) at lower hard costs, construction loan 10% (same model and assumptions as §6)

Hard $/sf ↓ · Sale $/sf →	$1,250	$1,350	$1,450	$1,550
$350	+$0.30M (+5.9%)	+$0.73M (+14.4%)	+$1.17M (+22.8%)	+$1.60M (+31.3%)
$400	+$0.00M (+0.1%)	+$0.44M (+8.1%)	+$0.87M (+16.1%)	+$1.30M (+24.1%)
$450	−$0.30M (−5.3%)	+$0.13M (+2.3%)	+$0.56M (+9.9%)	+$1.00M (+17.4%)

Reality check. Local data place $350/sf at the top of the semi-custom tier [N6, N7] and below the flood-zone custom range quoted in St. Pete [S1]; it is inside A2's elevated-waterfront range only at its low end [S3]. The recent sales that set $1,449–1,500/sf (323 Cordova, 1695 Brightwaters) are architect-designed homes with full custom finishes. A $350/sf home is more likely to be compared with $1,150–1,350/sf resales, where the margin falls to ≈0–8%. A practical target is ≈$400/sf with the structural and procurement levers applied and finish money concentrated in the kitchen, primary bath, entry and view wall.

Sources for this appendix

- **[N1]** NAHB, Cost of Constructing a Home 2024 (Jan 2025): https://www.nahb.org/news-and-economics/housing-economics-plus/special-studies/special-studies-pages/cost-of-constructing-a-home-in-2024
- **[N2]** Armor Pro Windows & Doors, impact window cost guide, Florida 2026 ($55–140/sf installed; pivot doors $5–12K+): https://www.armorprowindows.com/blog/impact-windows-cost-guide
- **[N3]** Armor Pro Windows & Doors, impact window cost by county, 2026 (sliders $80–200/sf): https://www.armorprowindows.com/blog/impact-window-cost-florida-by-county
- **[N4]** Florida Building Commission, Gulfside Elevator quote, 2-stop hydraulic home elevator $29,500 (hoistway by others): https://www.floridabuilding.org/fbc/commission/FBC_1225/Acc_Adv_Council/750/750_0_COST_EST_COMPLI_GulfsideElevatorQuote.pdf
- **[N5]** Estimate Florida Consulting, home elevator costs (hydraulic $27.5–55K): https://estimatorflorida.com/elevator-installation-cost-for-homes/
- **[N6]** Ben Laube Homes, production vs. semi-custom vs. custom, Florida: https://benlaubehomes.com/blog/semi-custom-vs-production-builder-florida
- **[N7]** NextLine Builders, cost to build in Tampa (2026): https://nextlinebuilders.com/cost-to-build-in/tampa/

N. Sources

Legend: [S#] = cited source · **[A]** = assumption · **TBD** = not yet known. Figures are desk estimates pending surveys, bids and quotes; not an appraisal or design. Photos of comparable homes are public listing images (MLS via BEX Realty), not the subject property.

- **[S1]** Revolution Florida, St. Pete custom home costs (Apr 2026): https://www.revolutionflorida.com/blog/custom-home-cost-guide
- **[S2]** St. Pete Home Guide, luxury custom builders, Snell Isle (updated Sep 28, 2026): https://stpetehomeguide.com/questions/luxury-custom-home-builders-st-pete-beach-snell-isle
- **[S3]** A2 Construction, Snell Isle costs (2026): https://www.a2constructionfl.com/blog/cost-build-custom-home-snell-isle
- **[S4]** GGC Construction, Tampa Bay waterfront costs (2026): https://ggcconstructiongroup.com/resources/waterfront-home-construction-cost-tampa
- **[S6]** LaBram Homes, coastal luxury from $650+/sf: https://labramhomes.com/how-much-does-it-cost-to-build-a-custom-home-in-tampa-bay/
- **[S7]** Sharper Image Pools, St. Pete: https://sharperimagepools.com/custom-pool-builder-st-petersburg/
- **[S8]** Pool Perfection, Tampa Bay: https://www.poolperfection.com/blog-post/how-much-does-it-cost-to-build-a-pool-in-tampa-bay
- **[S9]** FL Dept. of Revenue, documentary stamp tax (deed 0.70%, notes 0.35%) and nonrecurring intangible tax (0.2%): https://floridarevenue.com/taxes/taxesfees/pages/doc_stamp.aspx
- **[S10]** Jaken Finance Group, Florida spec construction loans (2026): https://jakenfinancegroup.com/spec-home-construction-loans-florida/
- **[S11]** Normandy, Florida spec home construction loans (prime + 2.95–3.95%; 75% LTC / 65% of value): https://normandy.com/builder-model-spec-loan/florida/
- **[S13]** Pinellas Tax Collector, 2025 millage (St. Petersburg total 19.9197): https://pinellastaxcollector.gov/pdfs/2025%20MILLAGE.pdf
- **[S14]** Pinellas commission rates: https://flatfeemlssells.com/realtor-commission/pinellas-county (buyer-side 2.5–3% assumed; no listing commission)
- **[S15]** Listing agent comp sheet, "1500 North Shore Drive NE" (Nov 19, 2025)
- **[S16]** Exacta Land Surveyors boundary survey #2212.3381 (signed Jan 2, 2023)
- **[S17]** Seller's proposed site plan on survey base (FF 11.1 ft; FEMA 2003 map)
- **[S18]** "Hardscape/Landscape Concept – Hudson," T.H. Davis, P.A., Landscape Architect
- **[S19]** Builder's risk rates, Florida: Bright Coast (Pinellas $2.50–6.00 per $100), https://brightcoastins.com/builders-risk-calculator ; Builders Risk Nerd (Pinellas $6–10 per $1,000), https://www.buildersrisknerd.com/florida/
- **[S20]** Florida promulgated title insurance rates, F.A.C. 69O-186.003
- **[S21]** Comp listing details and photos: BEX Realty MLS pages (e.g., https://www.bexrealty.com/Florida/St-Petersburg/2030-coffee-pot-boulevard-ne/)
- **[S22]** City of St. Petersburg, Single Family Home Permits layer (declared construction value): https://egis.stpete.org/arcgis/rest/services/ServicesDOTS/PermitsResidential/MapServer/2
- **[S23]** WSJ Money Rates, prime 7.00% effective Sep 17, 2026: https://www.wsj.com/market-data/bonds/moneyrates ; Bankrate WSJ prime (Oct 6, 2026): https://www.bankrate.com/rates/interest-rates/wall-street-prime-rate/
- **[S25]** CostToBuildHouse, Construction Loan Guide 2026: https://www.costtobuildhouse.com/blog/construction-loan-guide-2026
- **[S32]** Construction loan using land equity: https://kenclarkjr.com/construction-loan-land-equity ; land-loan conversion: https://waldev.com/land-loan-to-construction-loan-conversion/
- **[S36]** CommFi, seller-financed land with a construction loan: https://commficap.com/answers/seller-financing-land
- **[S37]** Capital Kings, Florida new construction loans (rates as of Oct 2026): https://capitalkings.co/loans/new-construction-florida
- **[S38]** BlackRock Mortgage, spec construction loans (Jan 2026 matrix): https://www.blackrockmortgage.com/spec-construction-loans/
- **[S39]** St. Petersburg City Code §16.20.010 (NT districts), building style and design standards: https://library.municode.com/fl/st._petersburg/codes/code_of_ordinances?nodeId=PTIISTPECO_CH16LADERE_S16.20.010NETRSIMIDINT
- **[S40]** City of St. Petersburg, NT Code Summary handout (Aug 2025): https://cms5.revize.com/revize/stpete/Business/Planning%20&%20Zoning/Land%20Development/NT%20Code%20Summary%2008%2004%2025%20HANDOUT_ADA.pdf
- **[S41]** River Hills Homes, how custom home builders charge (builder fees 10–20% of construction cost, ≈15% average): https://riverhillsbuilder.com/how-do-custom-home-builders-charge/ ; Frontier, general contractor fees 10–20% on a full build (2026): https://frontierloghomes.com/how-much-does-a-general-contractor-charge/
- **[S43]** Florida contractor-qualifier fees (monthly retainers $500–900 low volume, $1,000–2,000 mid, $2,500–5,000+ high volume; revenue-based 1–3%): https://contractorqualifierconnect.com/contractor-qualifier-cost/ ; practitioner reports $1,000–3,000/month or a % of contract: https://www.reddit.com/r/GeneralContractor/comments/1gvftpw/fl_gc_qualifier_rate/
- **[S44]** Fla. Stat. §489.1195 (qualifying agents responsible for supervising field work and finances), §489.129(1)(d) (discipline for assisting unlicensed contracting), §489.103(7) (owner-builder exemption excludes homes built for sale): https://www.flsenate.gov/Laws/Statutes/2026/489.1195 ; https://www.flsenate.gov/Laws/Statutes/2026/489.129 ; https://www.flsenate.gov/Laws/Statutes/2026/489.103
- **[S42]** 1700 N Shore Dr NE price history (sold Jun 17, 2015, $1,950,000, Stellar MLS #U7740395; built 2017, 6,915 sf): https://www.trulia.com/home/1700-n-shore-dr-ne-saint-petersburg-fl-33704-164056245